



EXPERIENCE MALACCA

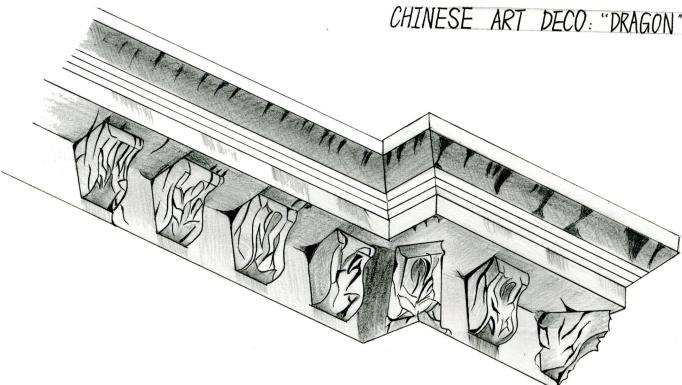


CHINESE ART DECO: "DRAGON"




DENTIL MOULDING

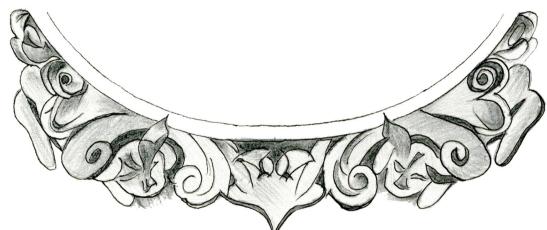

CHINESE ART DECO: "BAT"

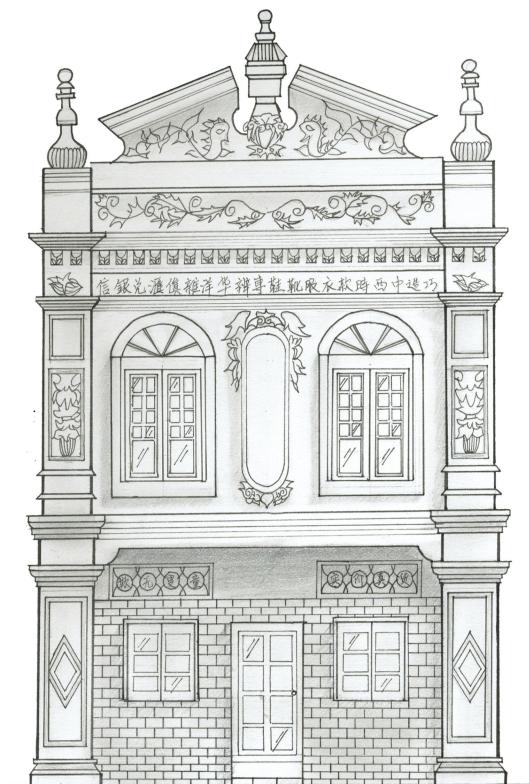

SHOPHOUSE ELEVATION
SCALE : 1:50

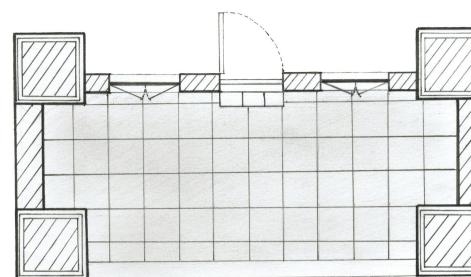

FRONT DOOR PLAN VIEW
SCALE : 1:50

THIS IS A CHINESE SHOPHOUSE AMONG A STREET OF HERITAGE ARCHITECTURE. THE FAÇADE IS HEAVILY DECORATED WITH CORINTHIAN PILASTERS AND LOUVRED FRENCH WINDOWS. THE SHOPHOUSE WAS USED AS A BANK AND A CLOTHING STORE BEFORE.



CHARACTER "ZHEN" ON WOODEN CHINESE SINGBOARD






ORNAMENTATION SHOWING "PHALLICISM"

THRESHOLD SPACE


INVESTIGATING THRESHOLD SPACE IN SHOPHOUSE
USING THREE SHOPHOUSES AT HIRON ROAD AS SAMPLES.

ANALYSIS

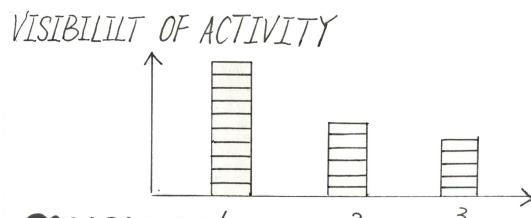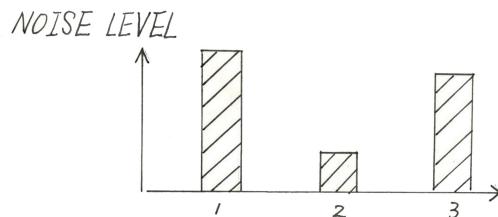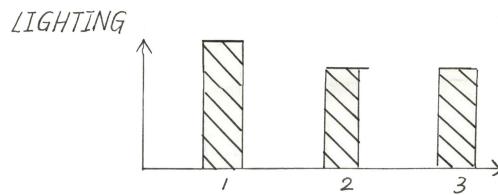


CONCLUSION






IN ORDER TO MAKE THE STORE MORE INVITING, ONE CAN INCREASE THE LIGHTING, NOISE LEVEL AND THE VISIBILITY OF ACTIVITY.

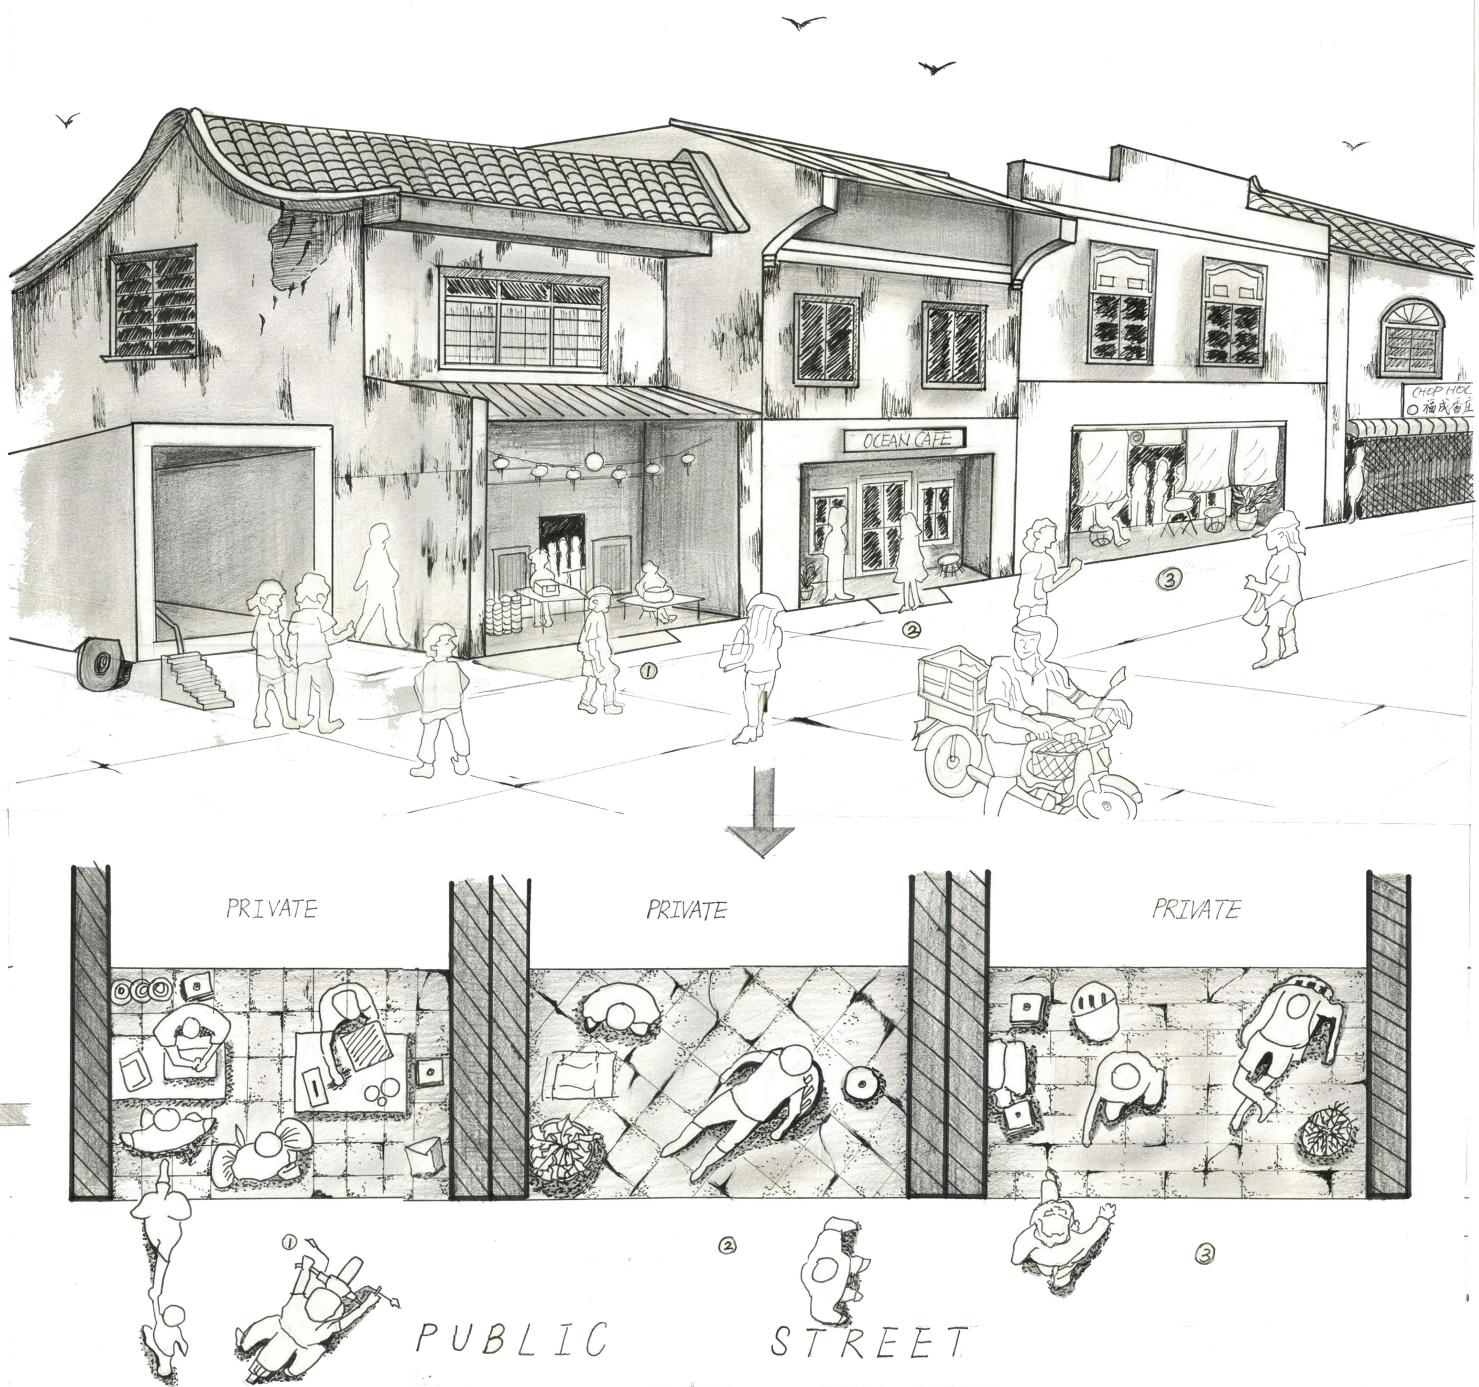

MALACCA, MY

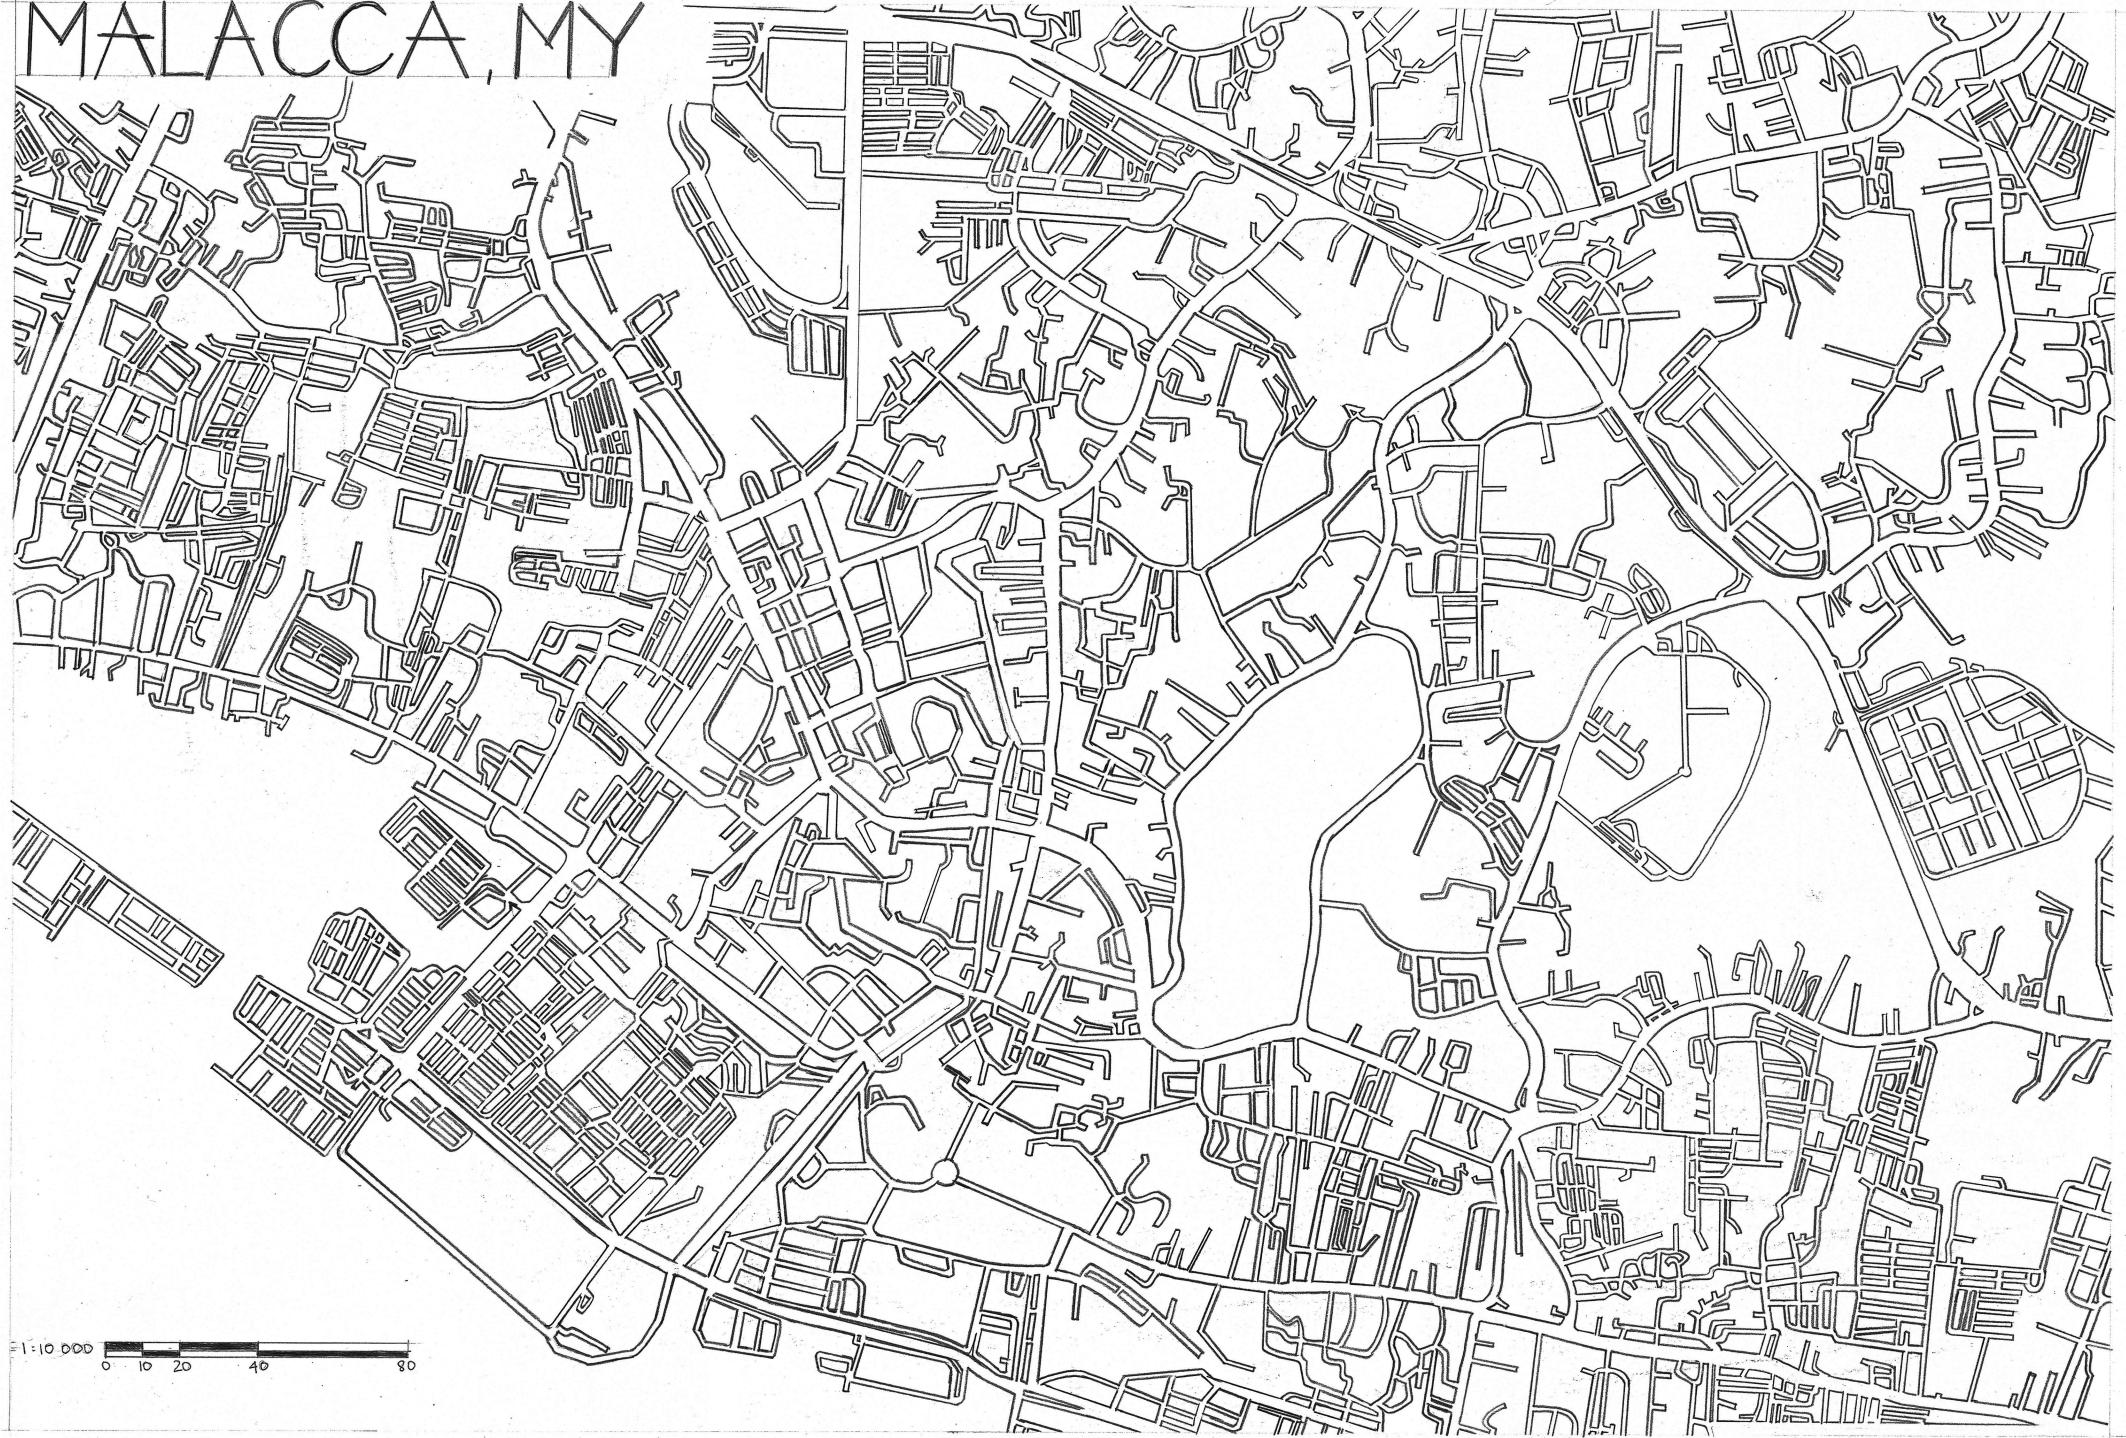

STREET ELEVATIONS AND SECTION

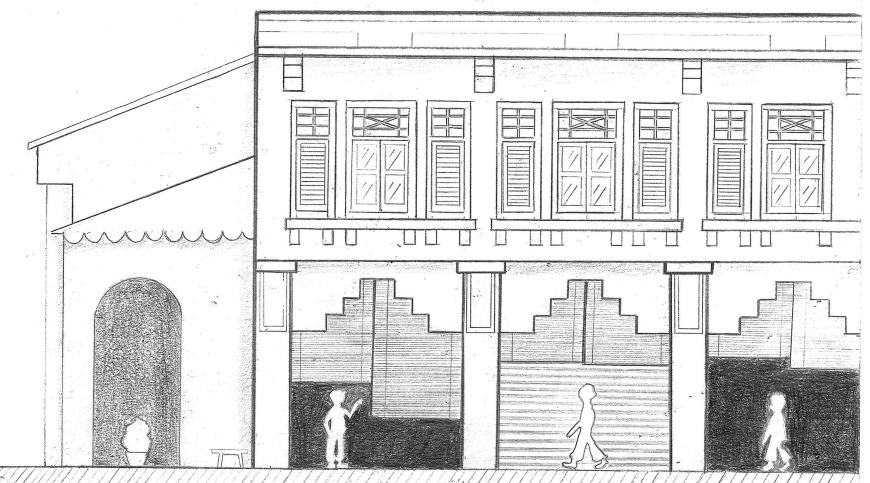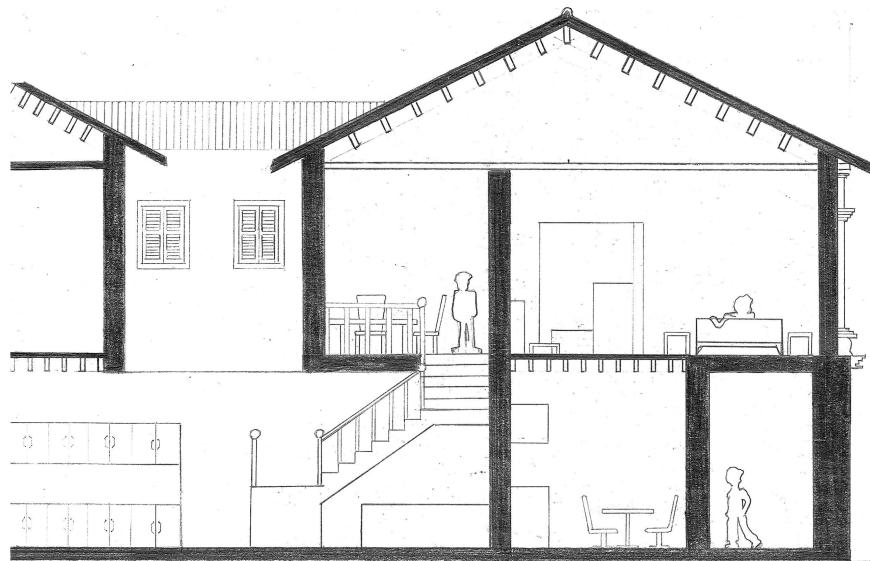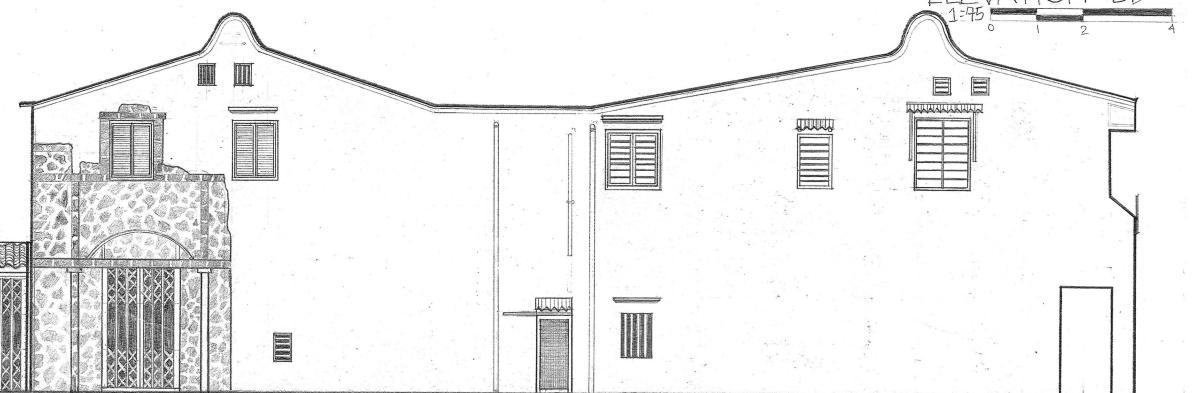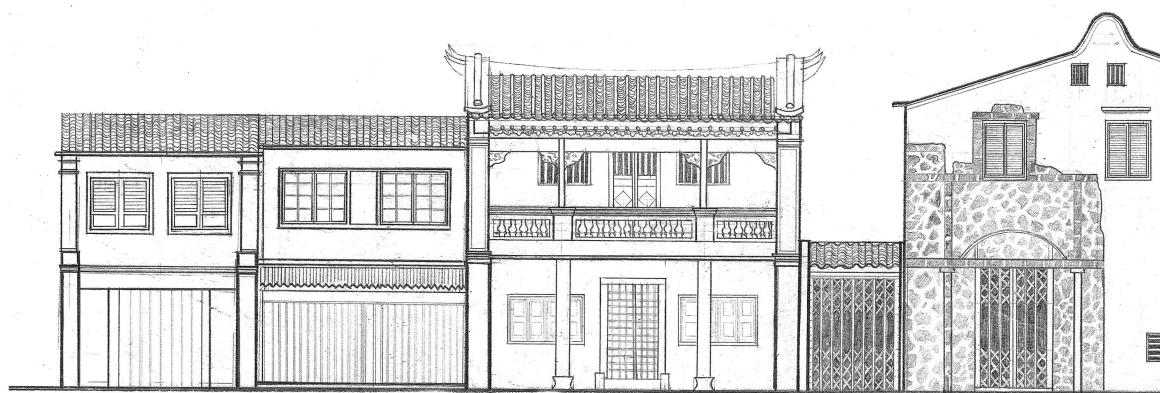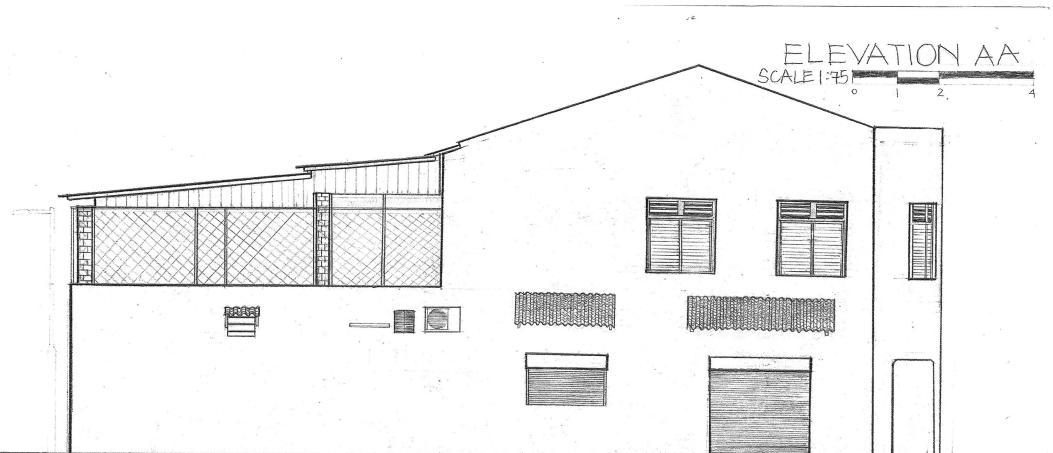

JALAN HANG KATSURI

■ AREA KNOWN FOR
LOCAL TRADES
AND CRAFTS




FIGURE GROUND
SCALE 1:3000 0 3 6 12 24

JALAN HANG KATSURI IS A STREET CONNECTING THE THREE MAIN TOURIST STREETS – JALAN TUN TAN CHENG LOCK, JALAN HANG JEBAT (JONKER ST.), AND JALAN TUKANG BESI.



ITS UNIQUE FEATURE IS THE MANY LOCAL TRADES AND CRAFTS SITUATED ALONG THIS STREET, CONTRASTING WITH THE HYPER-COMMERCIALIZED TOURIST AREAS NEARBY.




RESIDENTS RUN THEIR HUMBLE BUSINESSES ON THE FIRST FLOOR AND LIVE ON THE SECOND. MOST PEDESTRIANS ARE IN TRANSIT AND FEW STOP ALONG THE STREET.

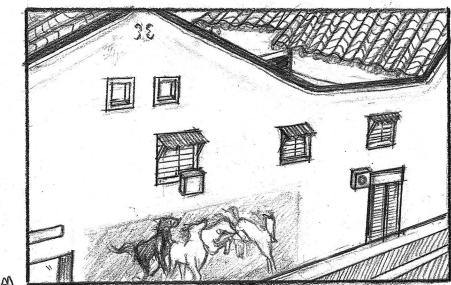

A LARGE MURAL OF GALLOPING HORSES BY RENOWNED ARTISTS CHONG CHEN CHUAN AND QUAKE KAH ANN, THEMED "TOWARDS A NEW JOURNEY". IT IS ONE OF THE MOST POPULAR MURALS IN MALACCA.

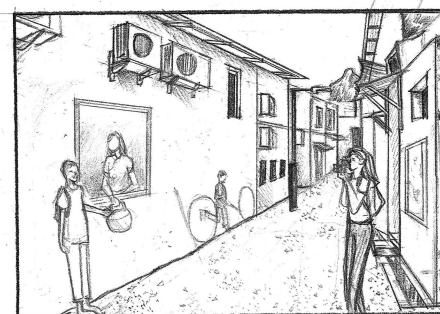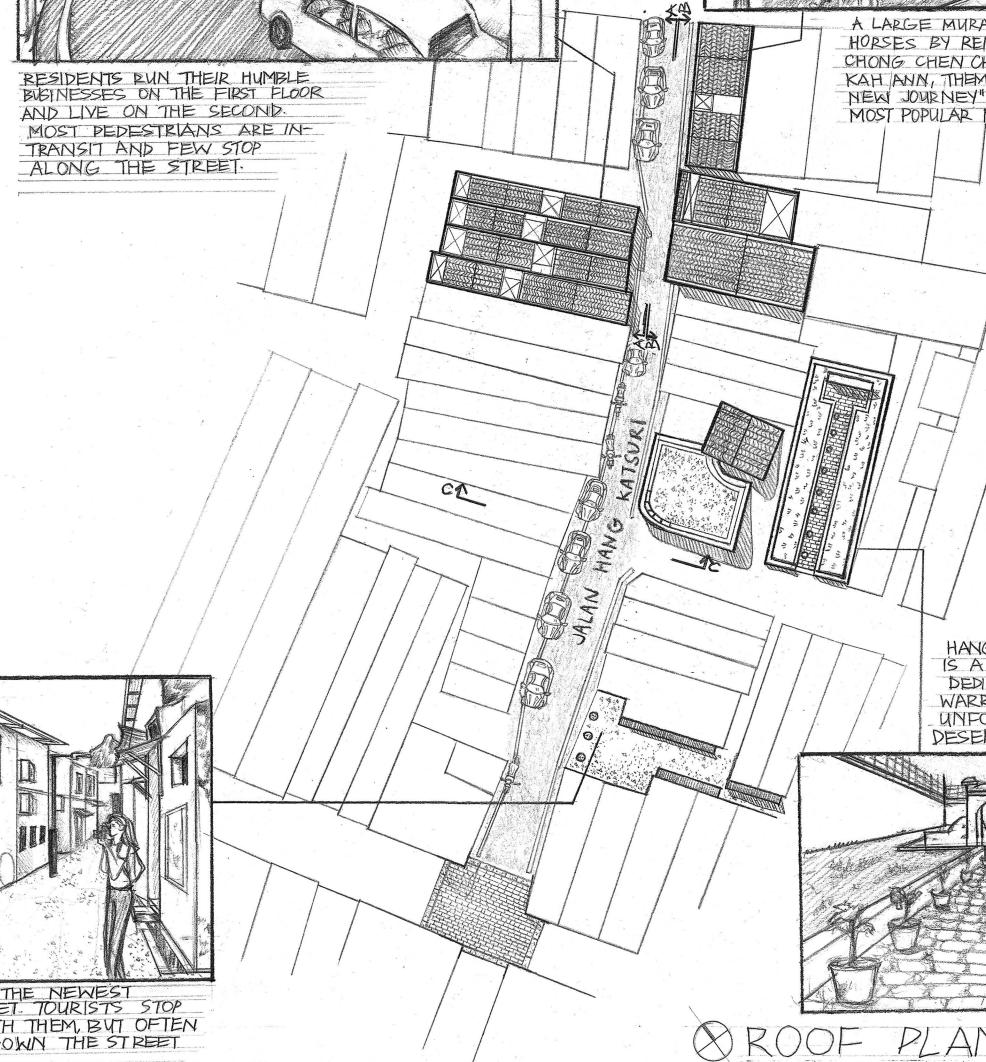

THESE MURALS ARE THE NEWEST ADDITION TO THE STREET. TOURISTS STOP TO TAKE PHOTOS WITH THEM, BUT OFTEN DO NOT VENTURE DOWN THE STREET BEYOND THE MURALS.

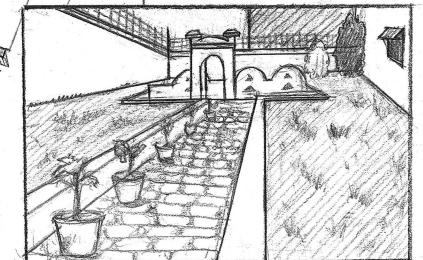

ROOF PLAN
SCALE 1:500 0 5 10 20 40

HANG JEBAT MAUSOLEUM IS A BURIAL GROUND DEDICATED TO LEGENDARY WARRIOR HANG JEBAT. UNFORTUNATELY, IT SEEMED DESERTED AND EMPTY.