



SITE ANALYSIS


THE SITE IS AT DIARY FARM WITH VARIOUS TYPES OF FLORA AND FAUNA. WITH ITS TYPOLOGY SLIGHTLY LOWER THAN THE SURROUNDING AREA. IT IS HIDDEN FROM THE MAIN PUBLIC ROAD. HOWEVER, CLOSER TO THE MOUNTAIN BIKING TRAIL AND HIKING TRAIL. IT IS EASILY ACCESSIBLE FROM BOTH NORTH AND WEST DIRECTION.

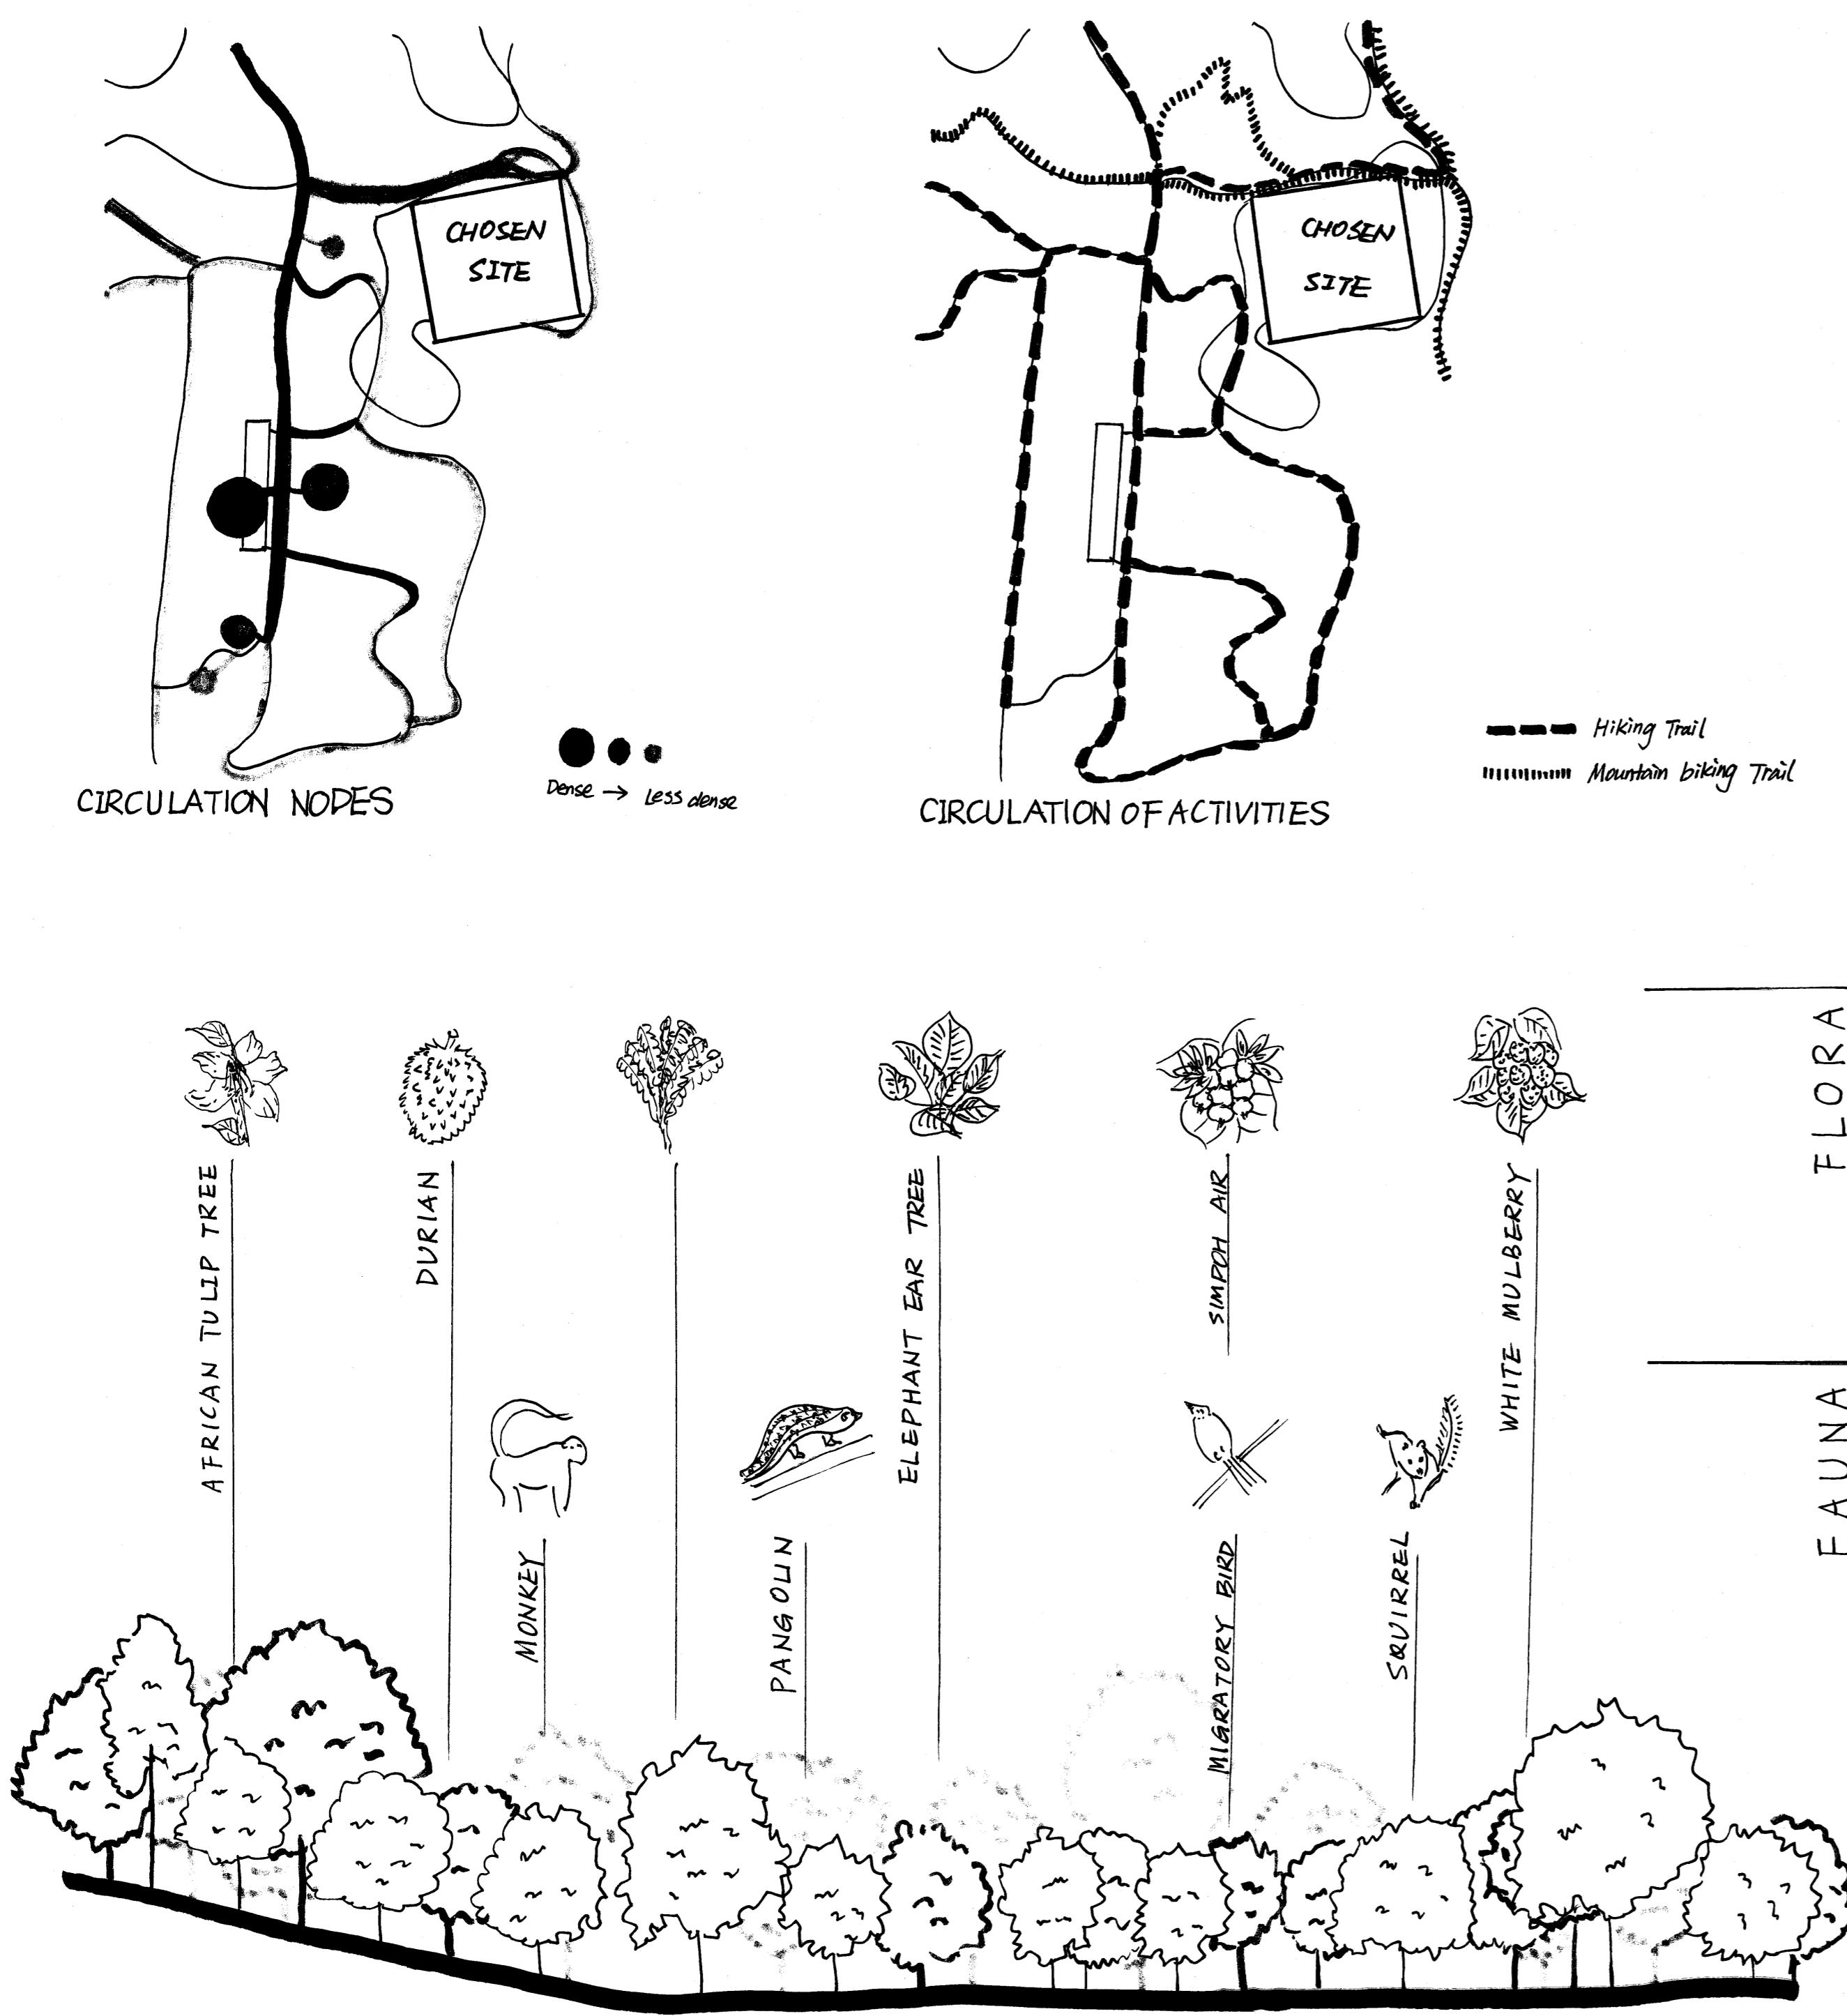


CONCEPT DEVELOPMENT

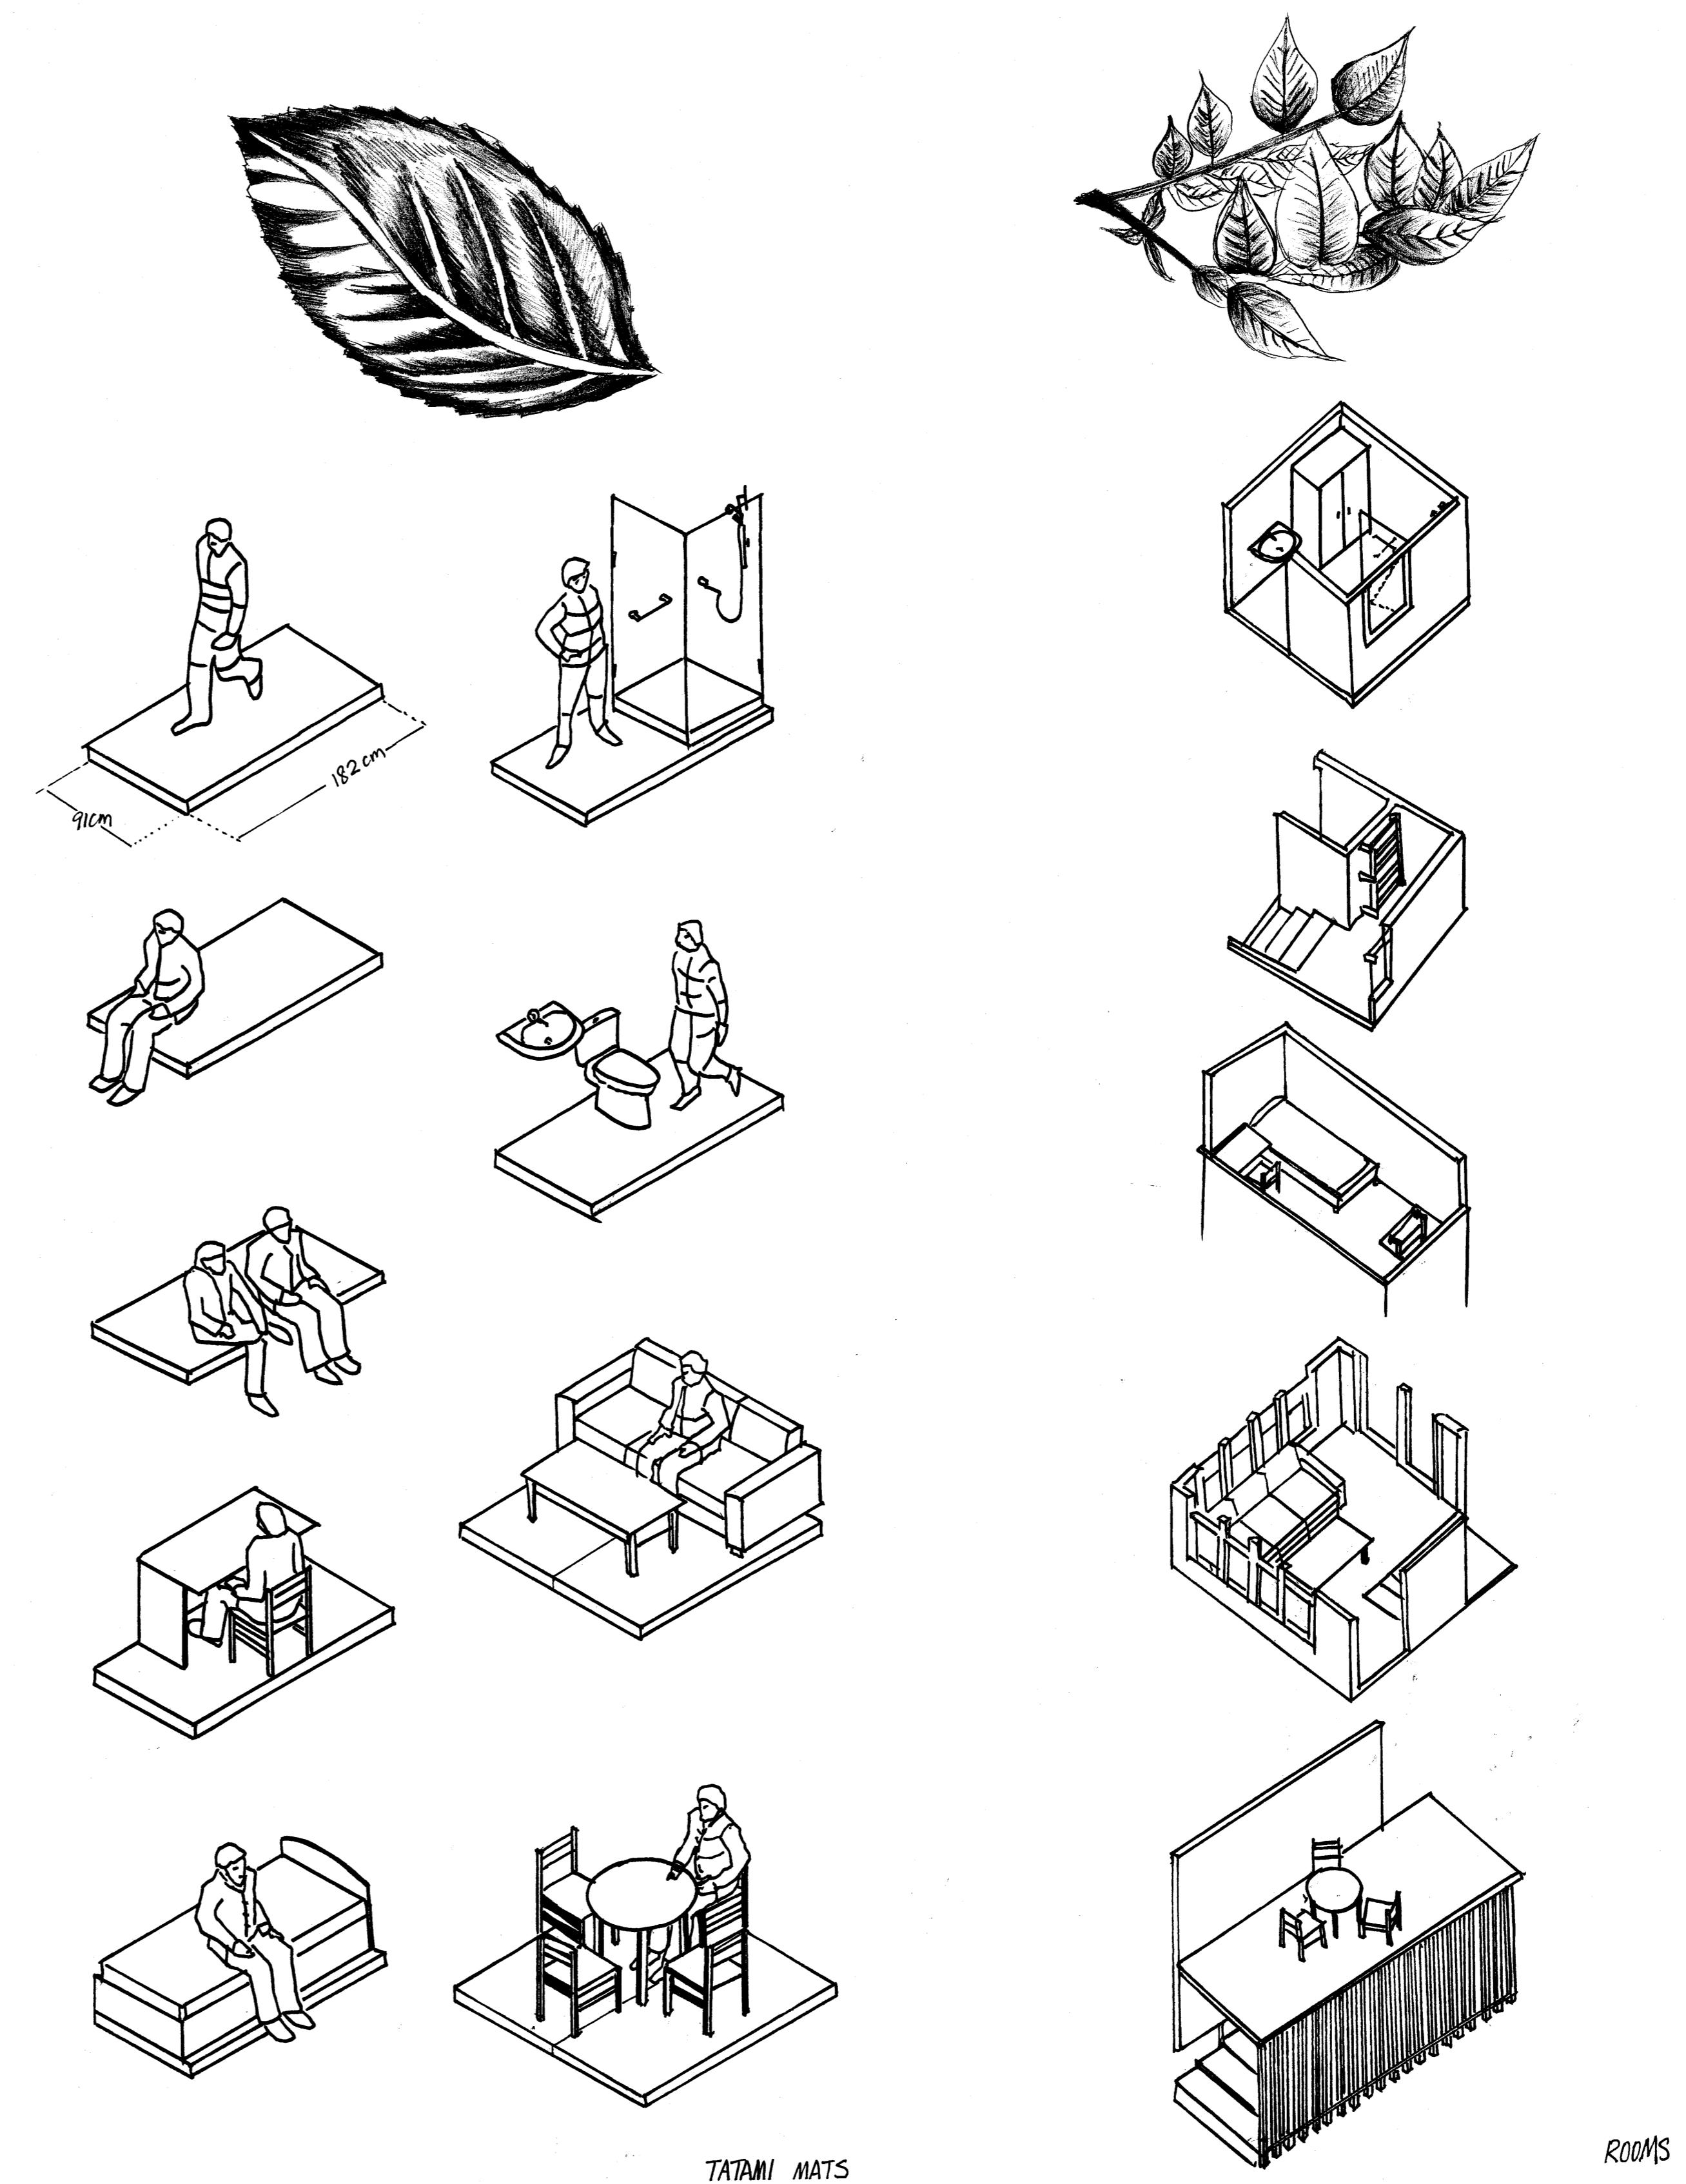

MODULE DEVELOPMENT

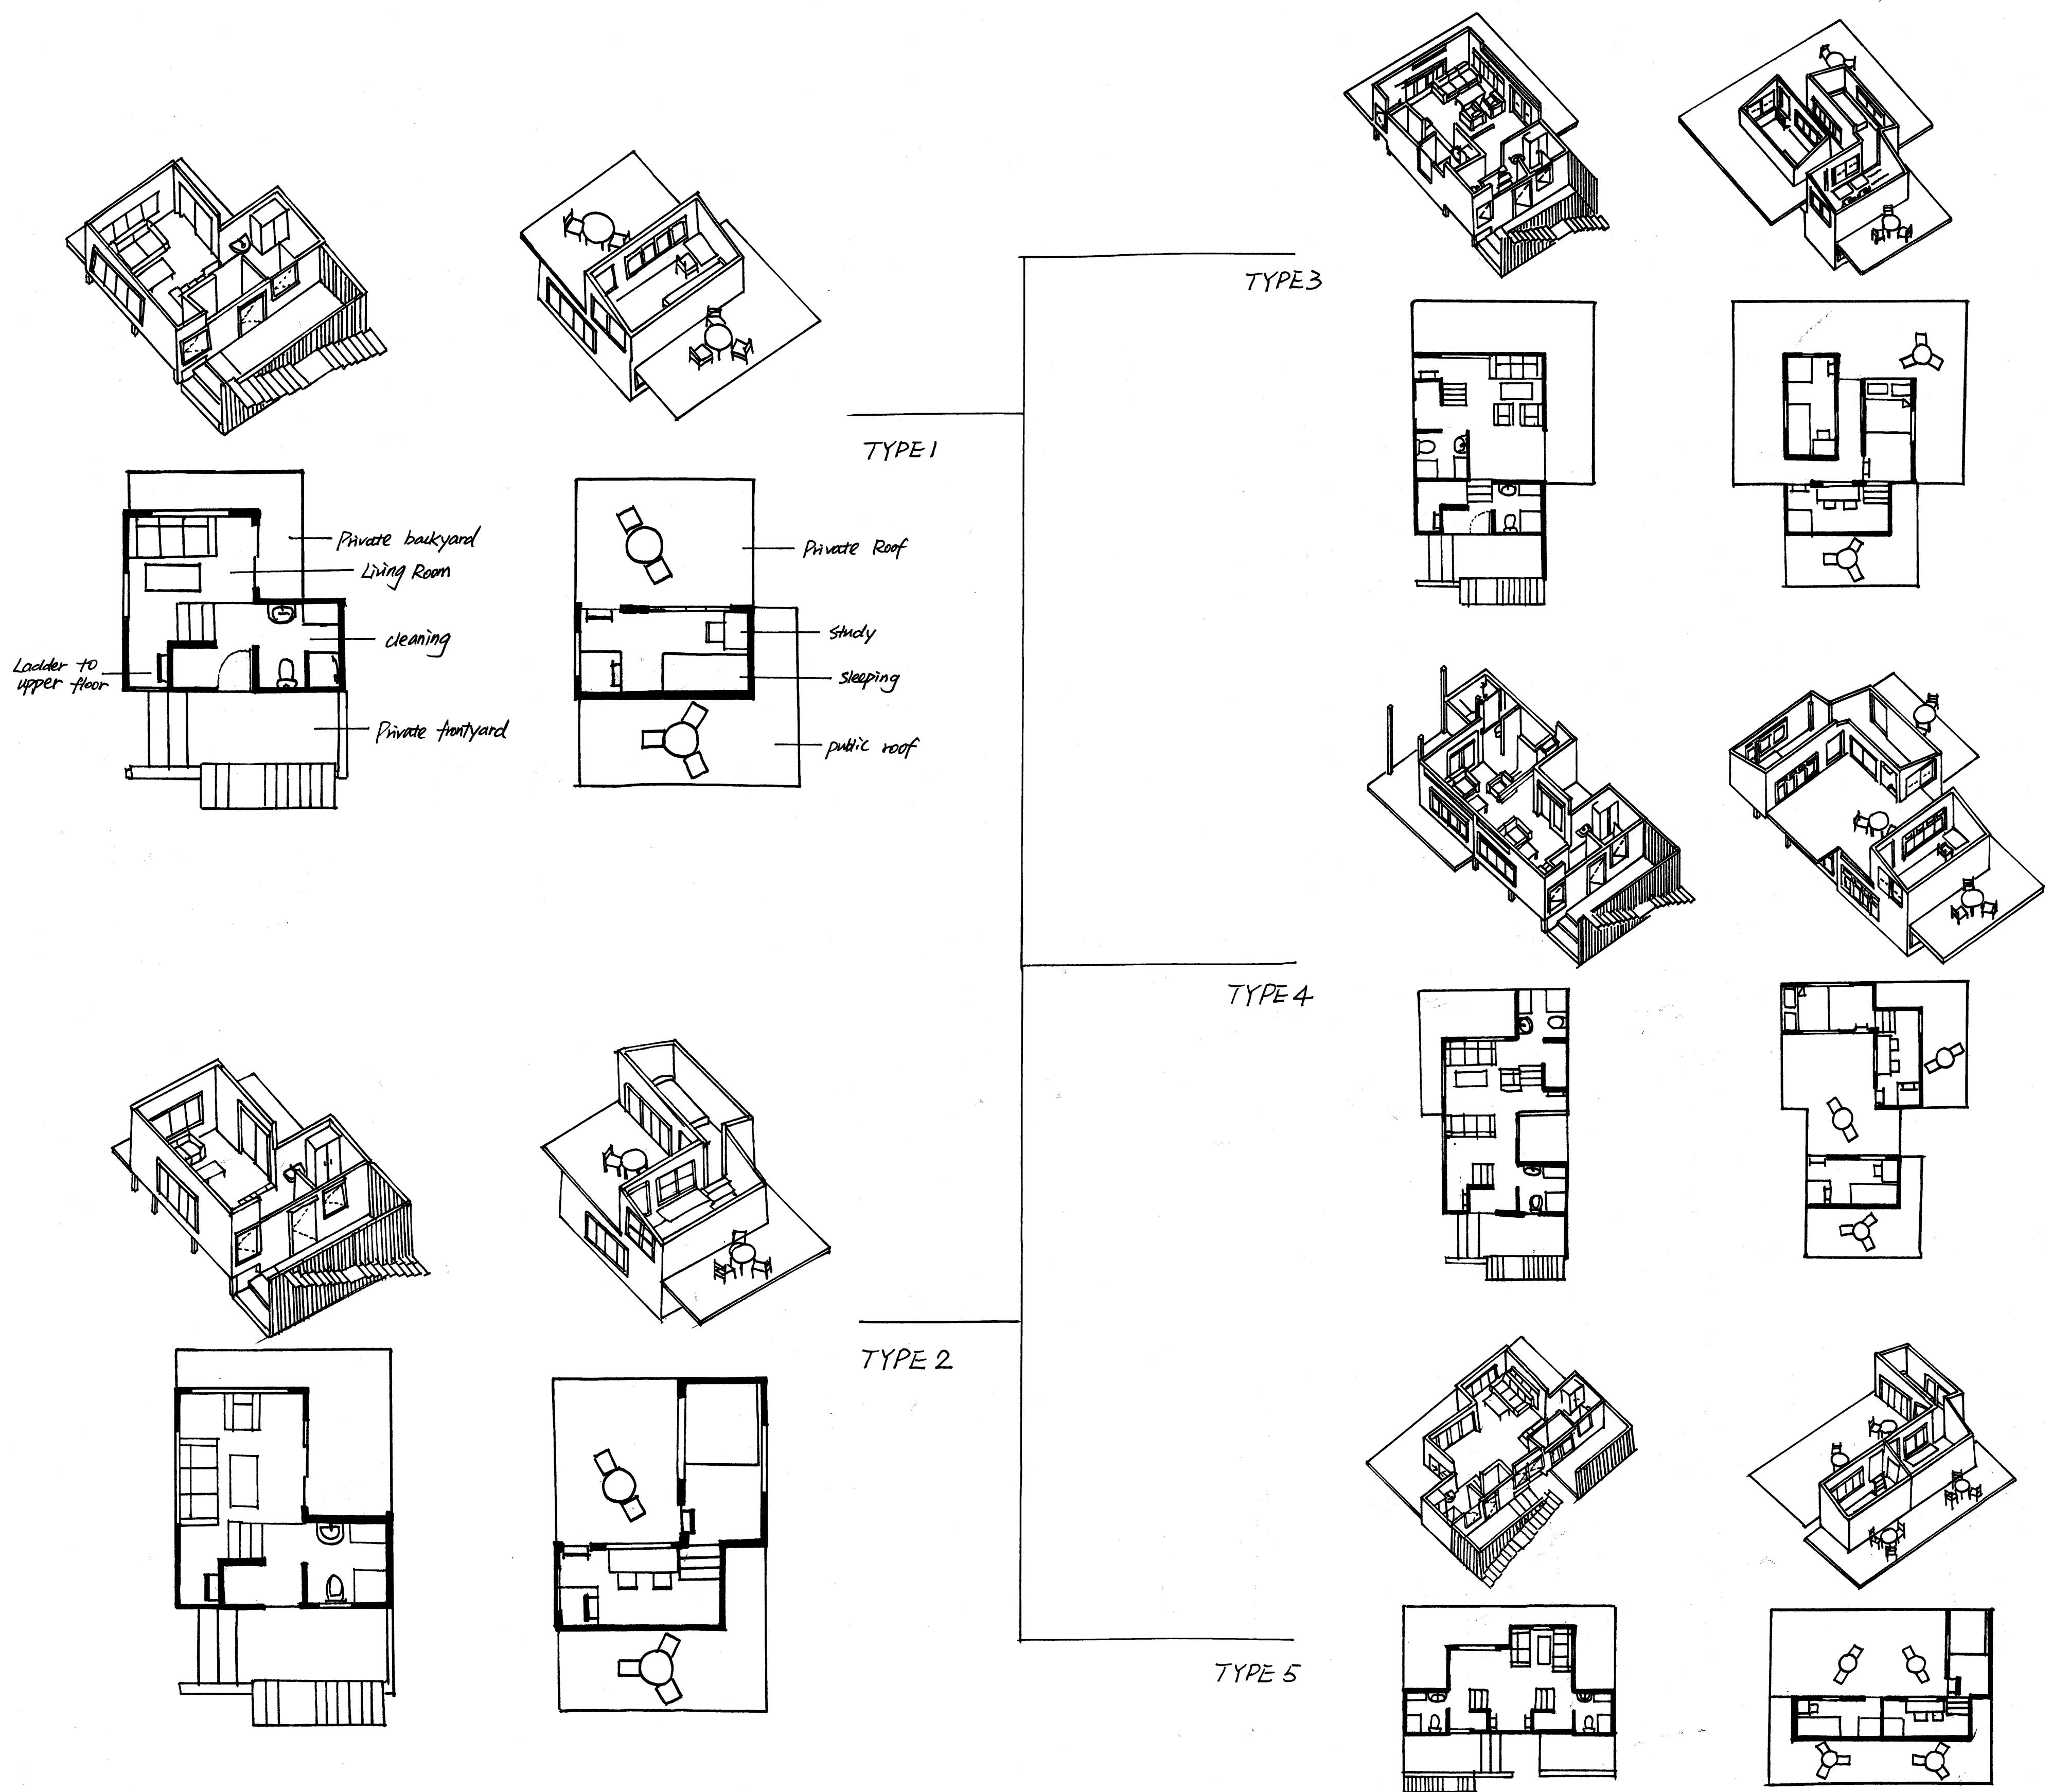

PLAN, SECT

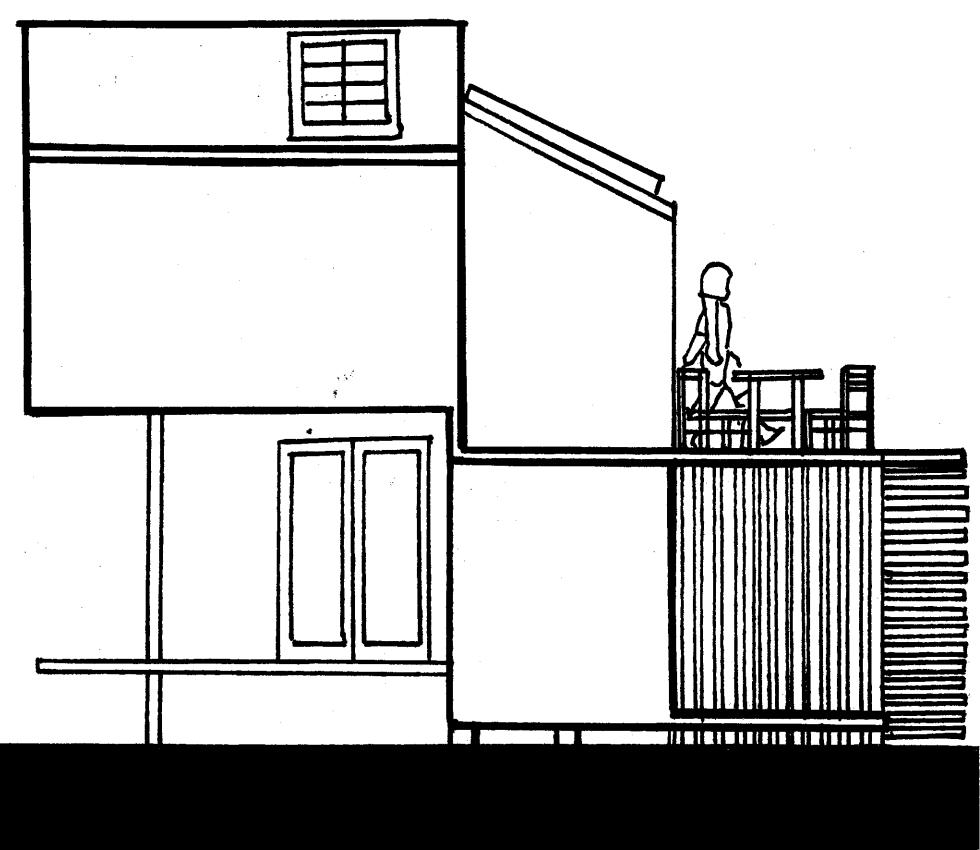


E-01




S-01




E-02

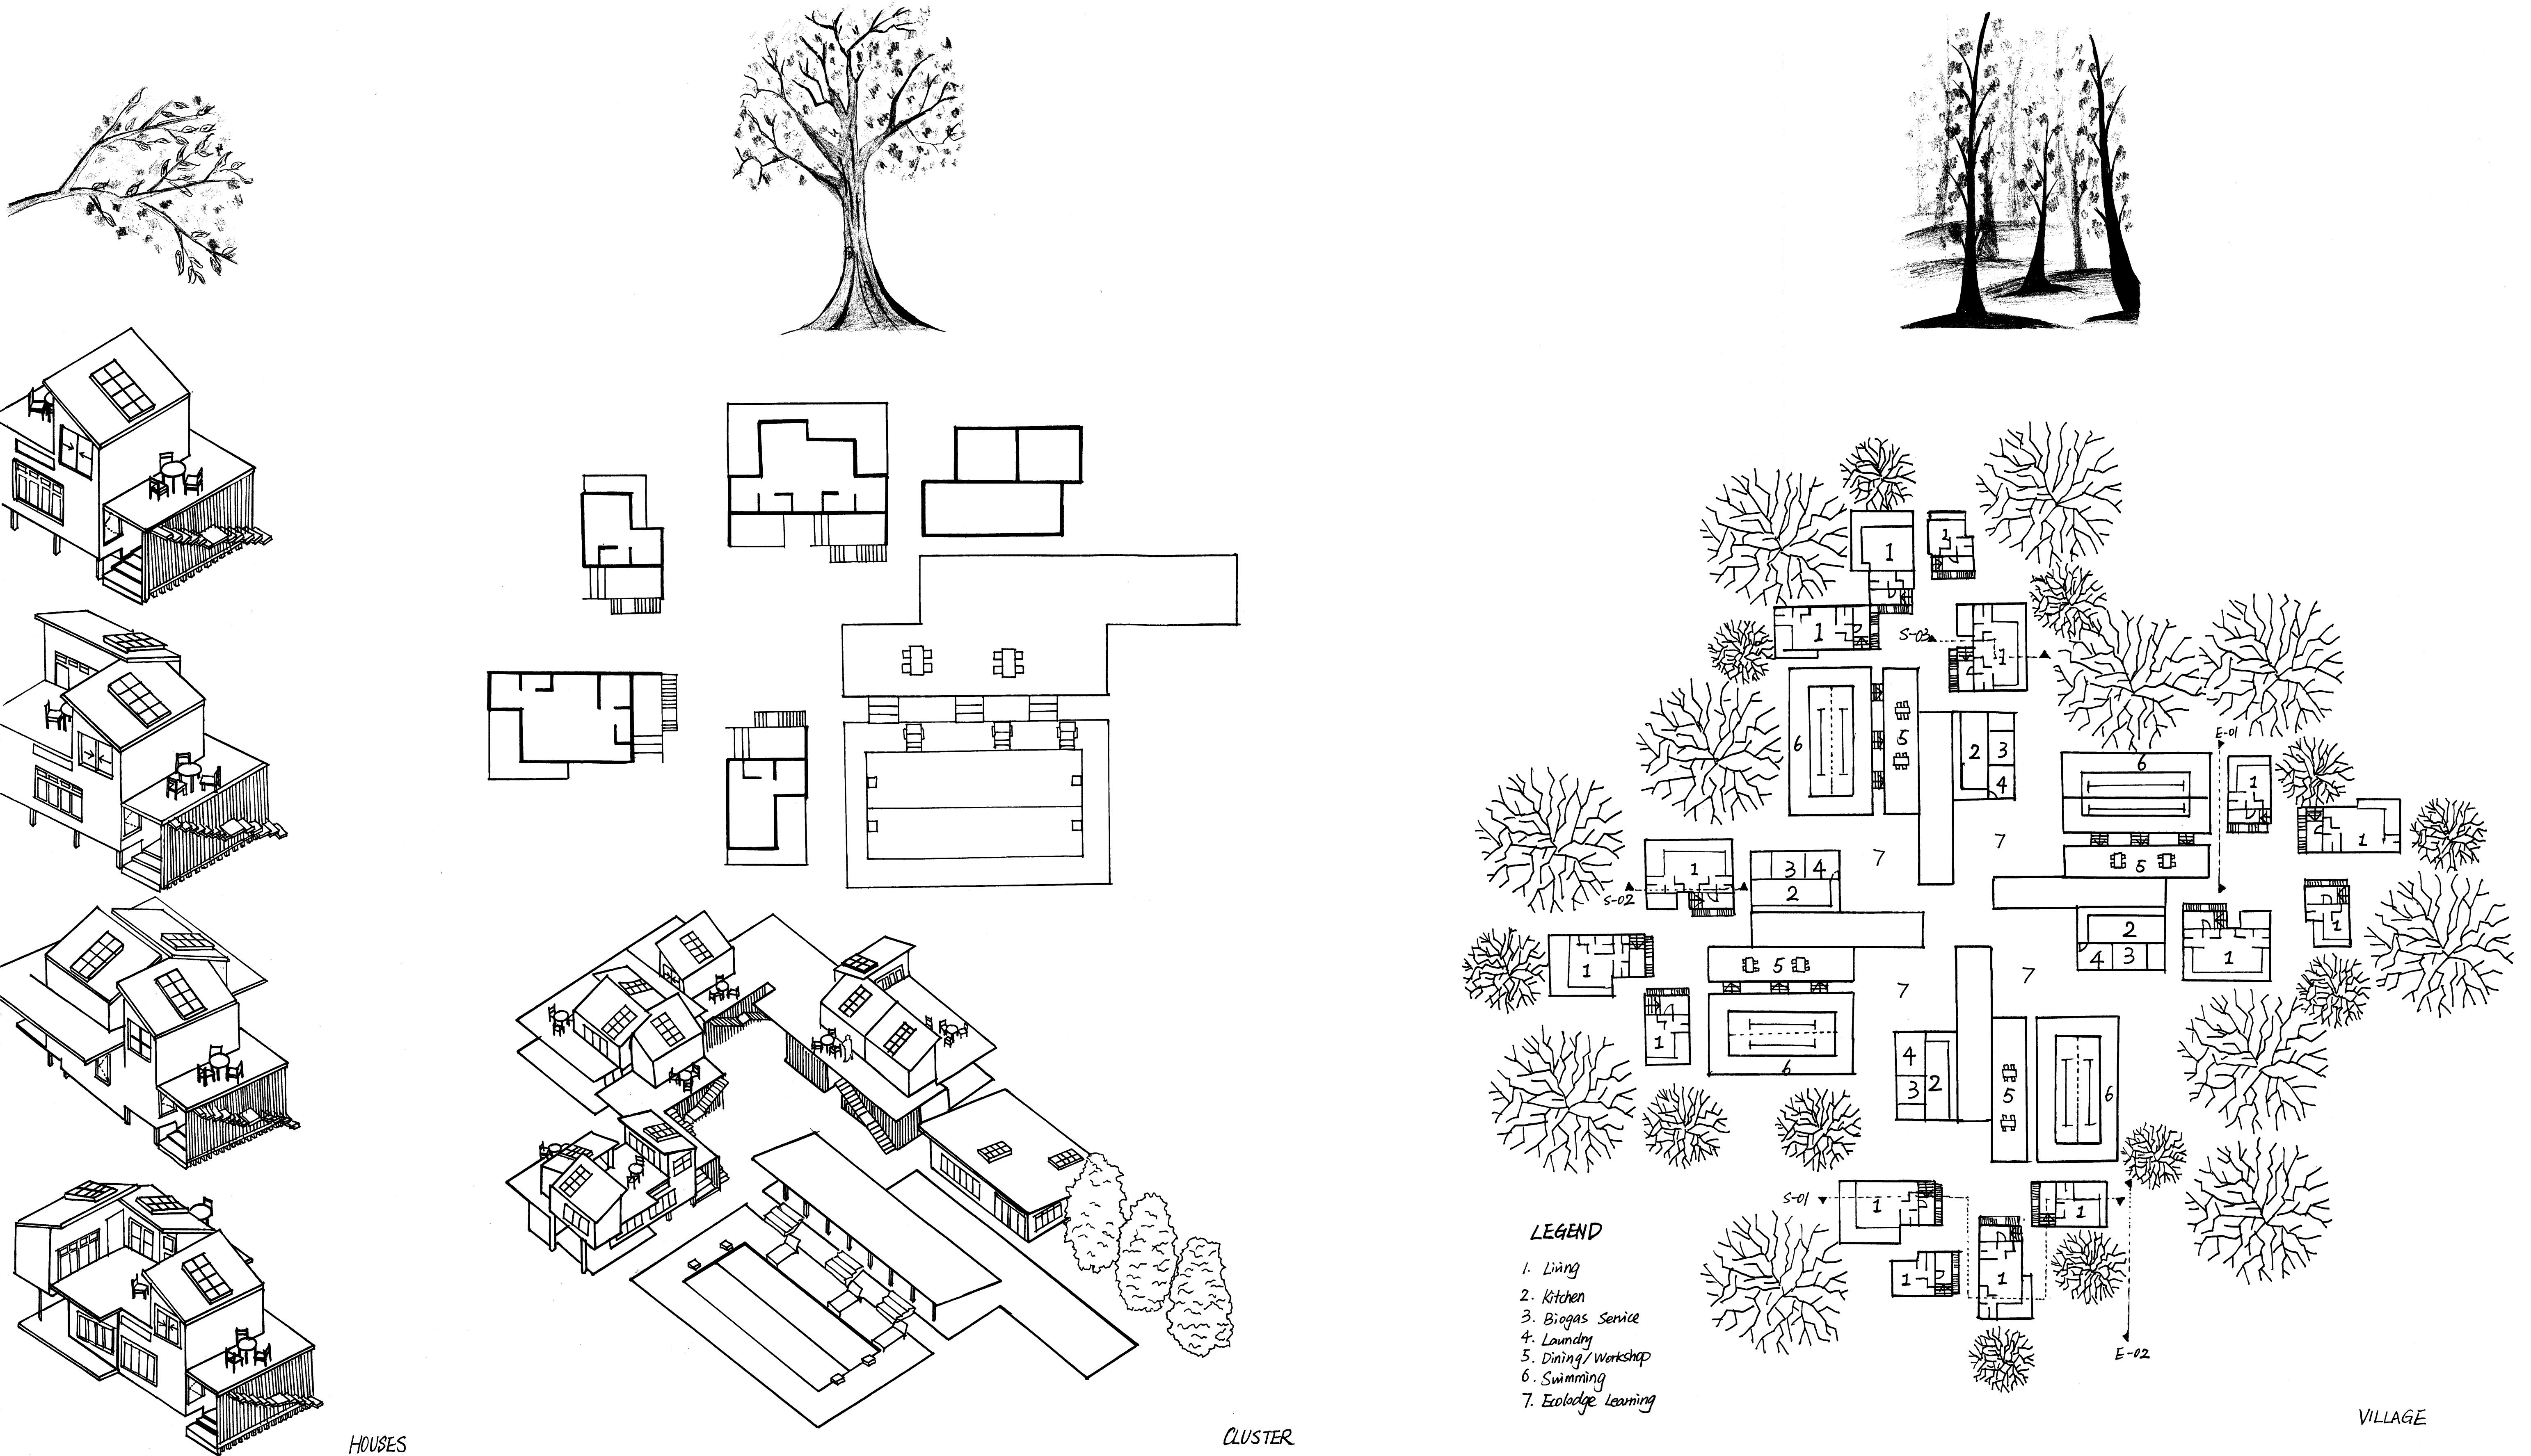


ION, ELEVATION

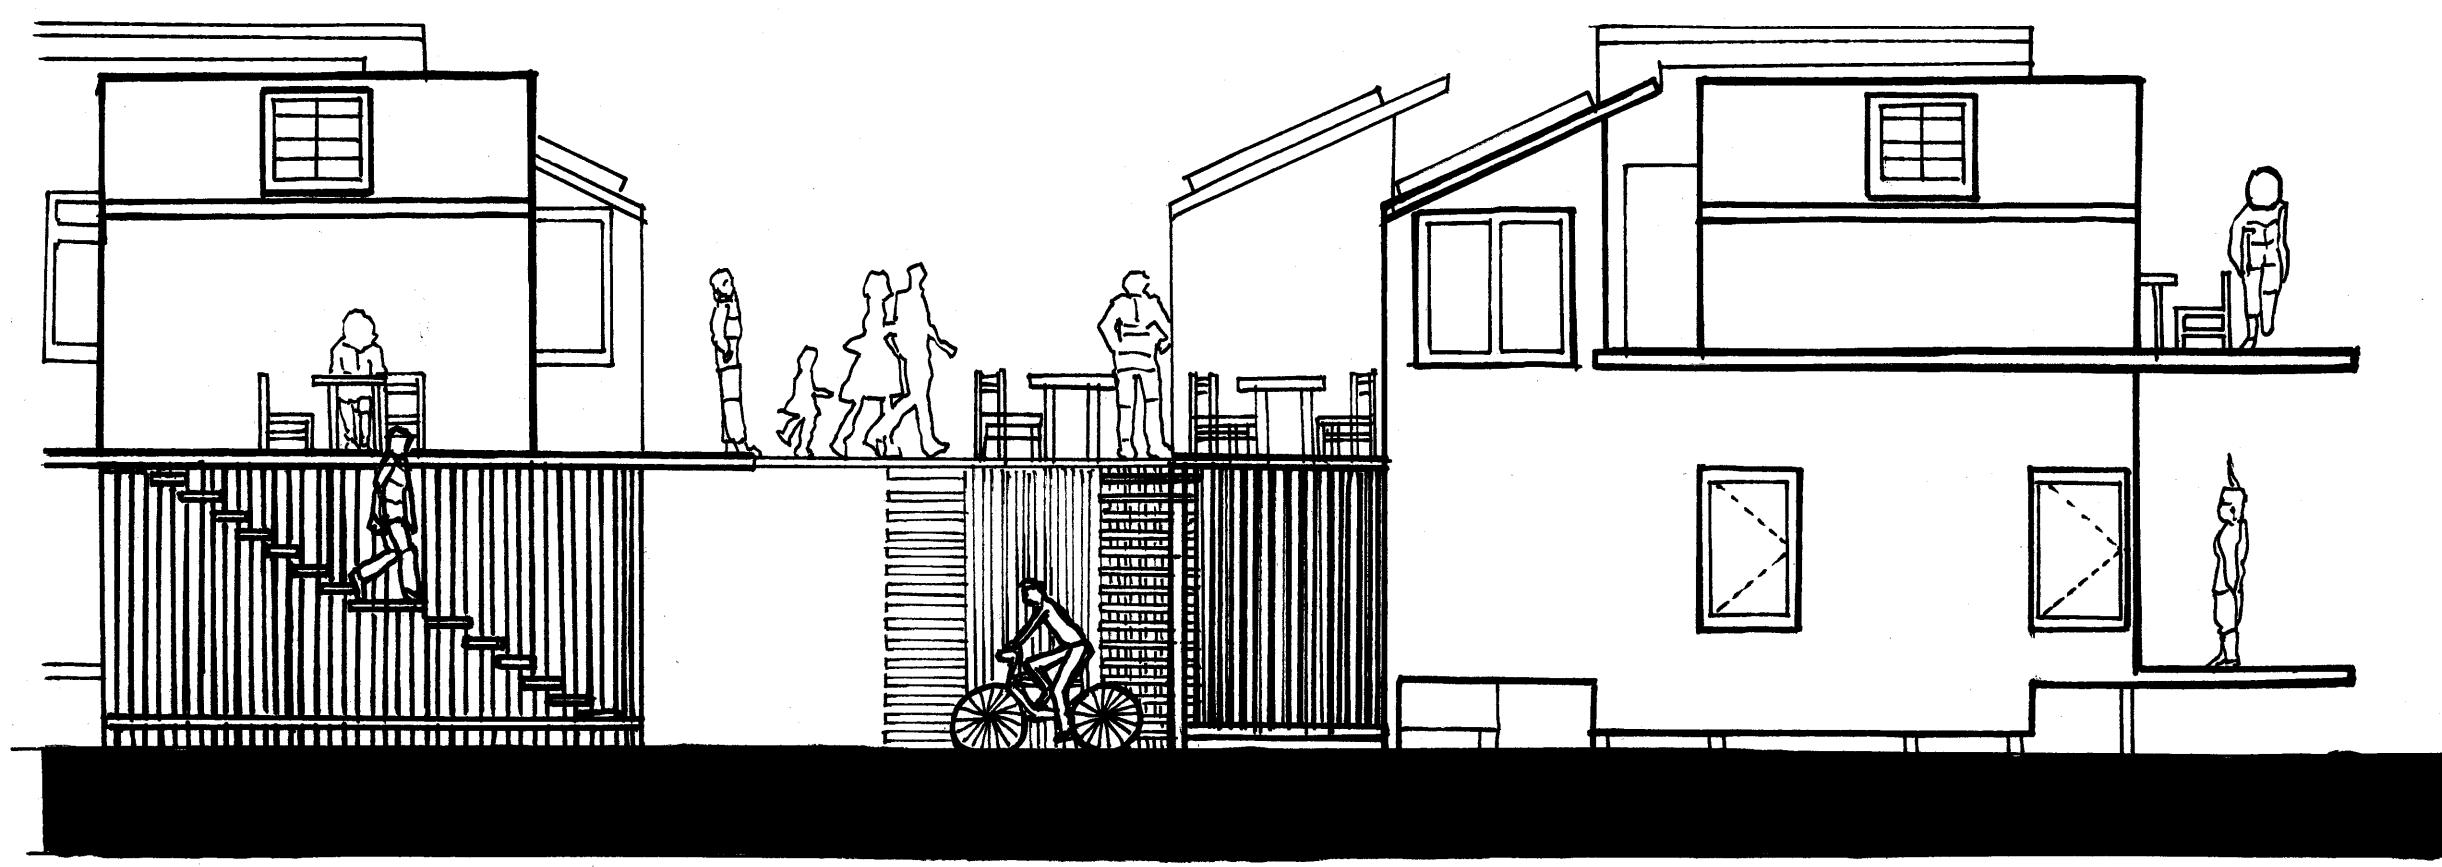


1:100

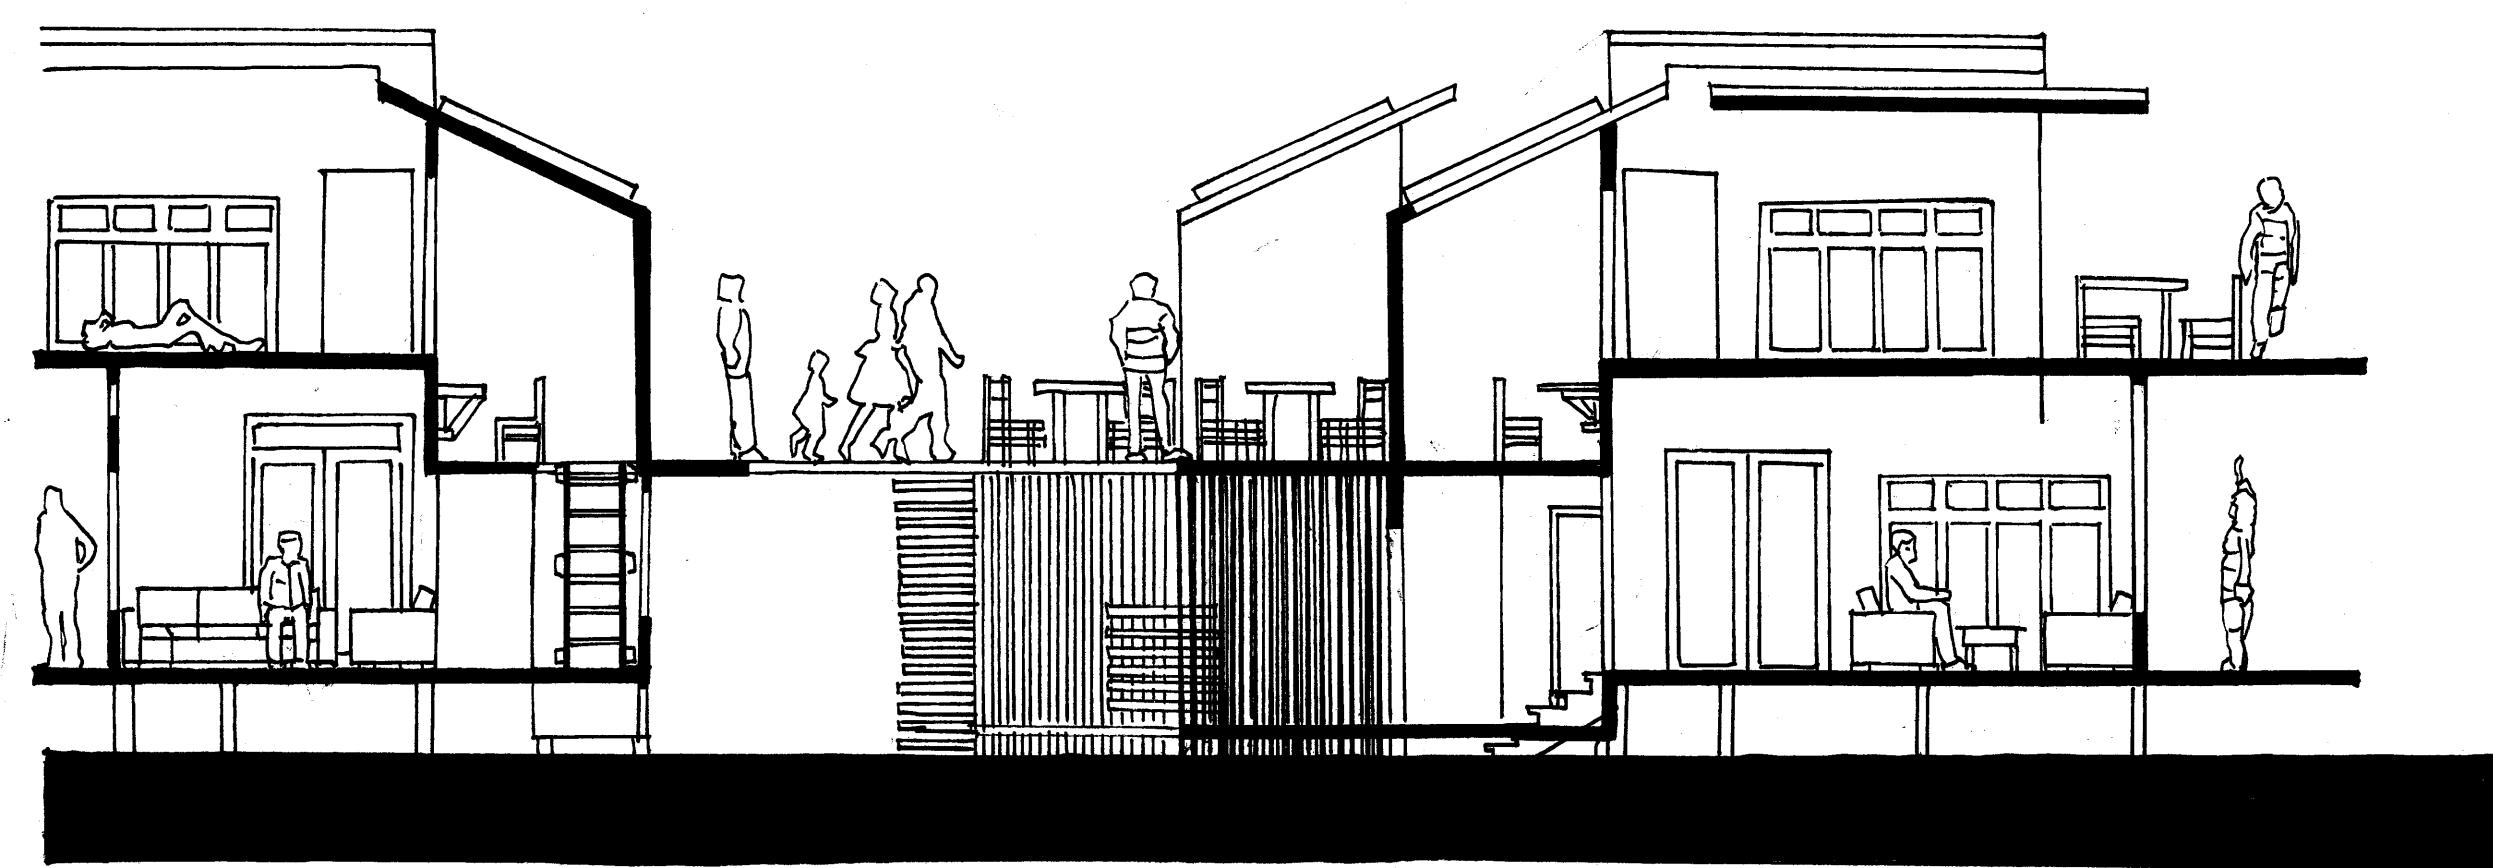


1:100

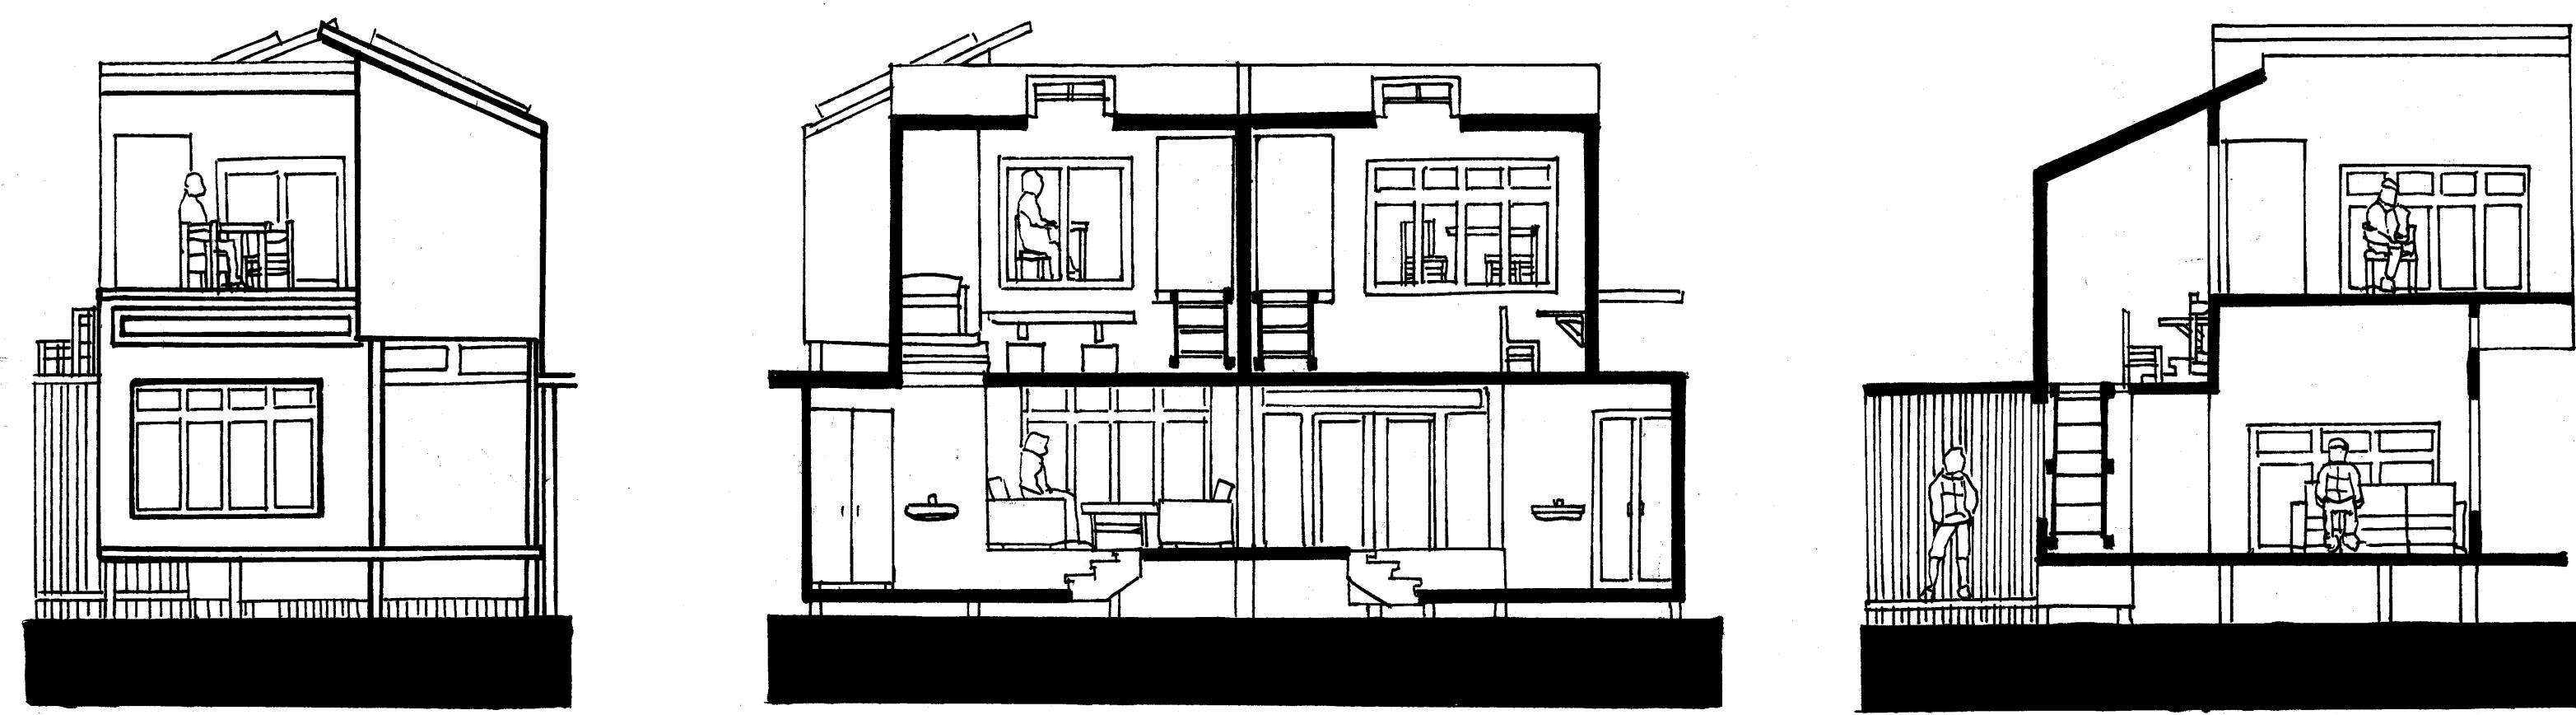

1:100

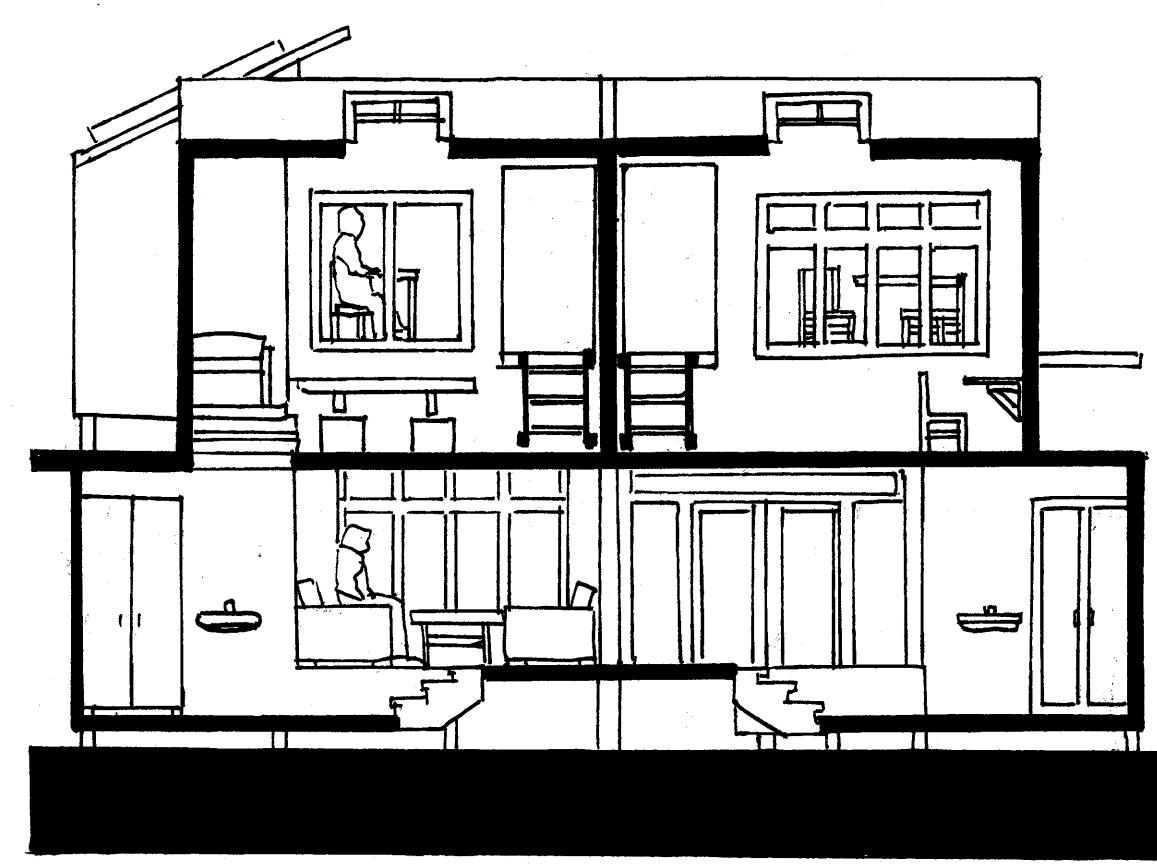


S-02

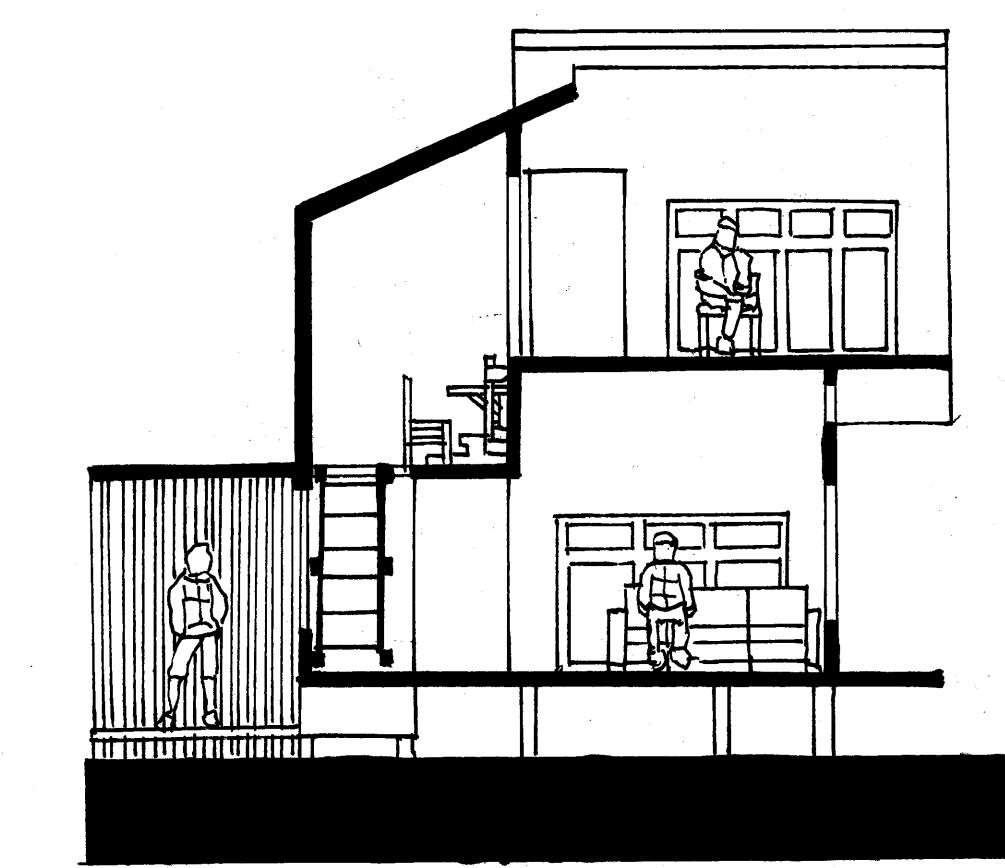


1:100

S-03

1:100



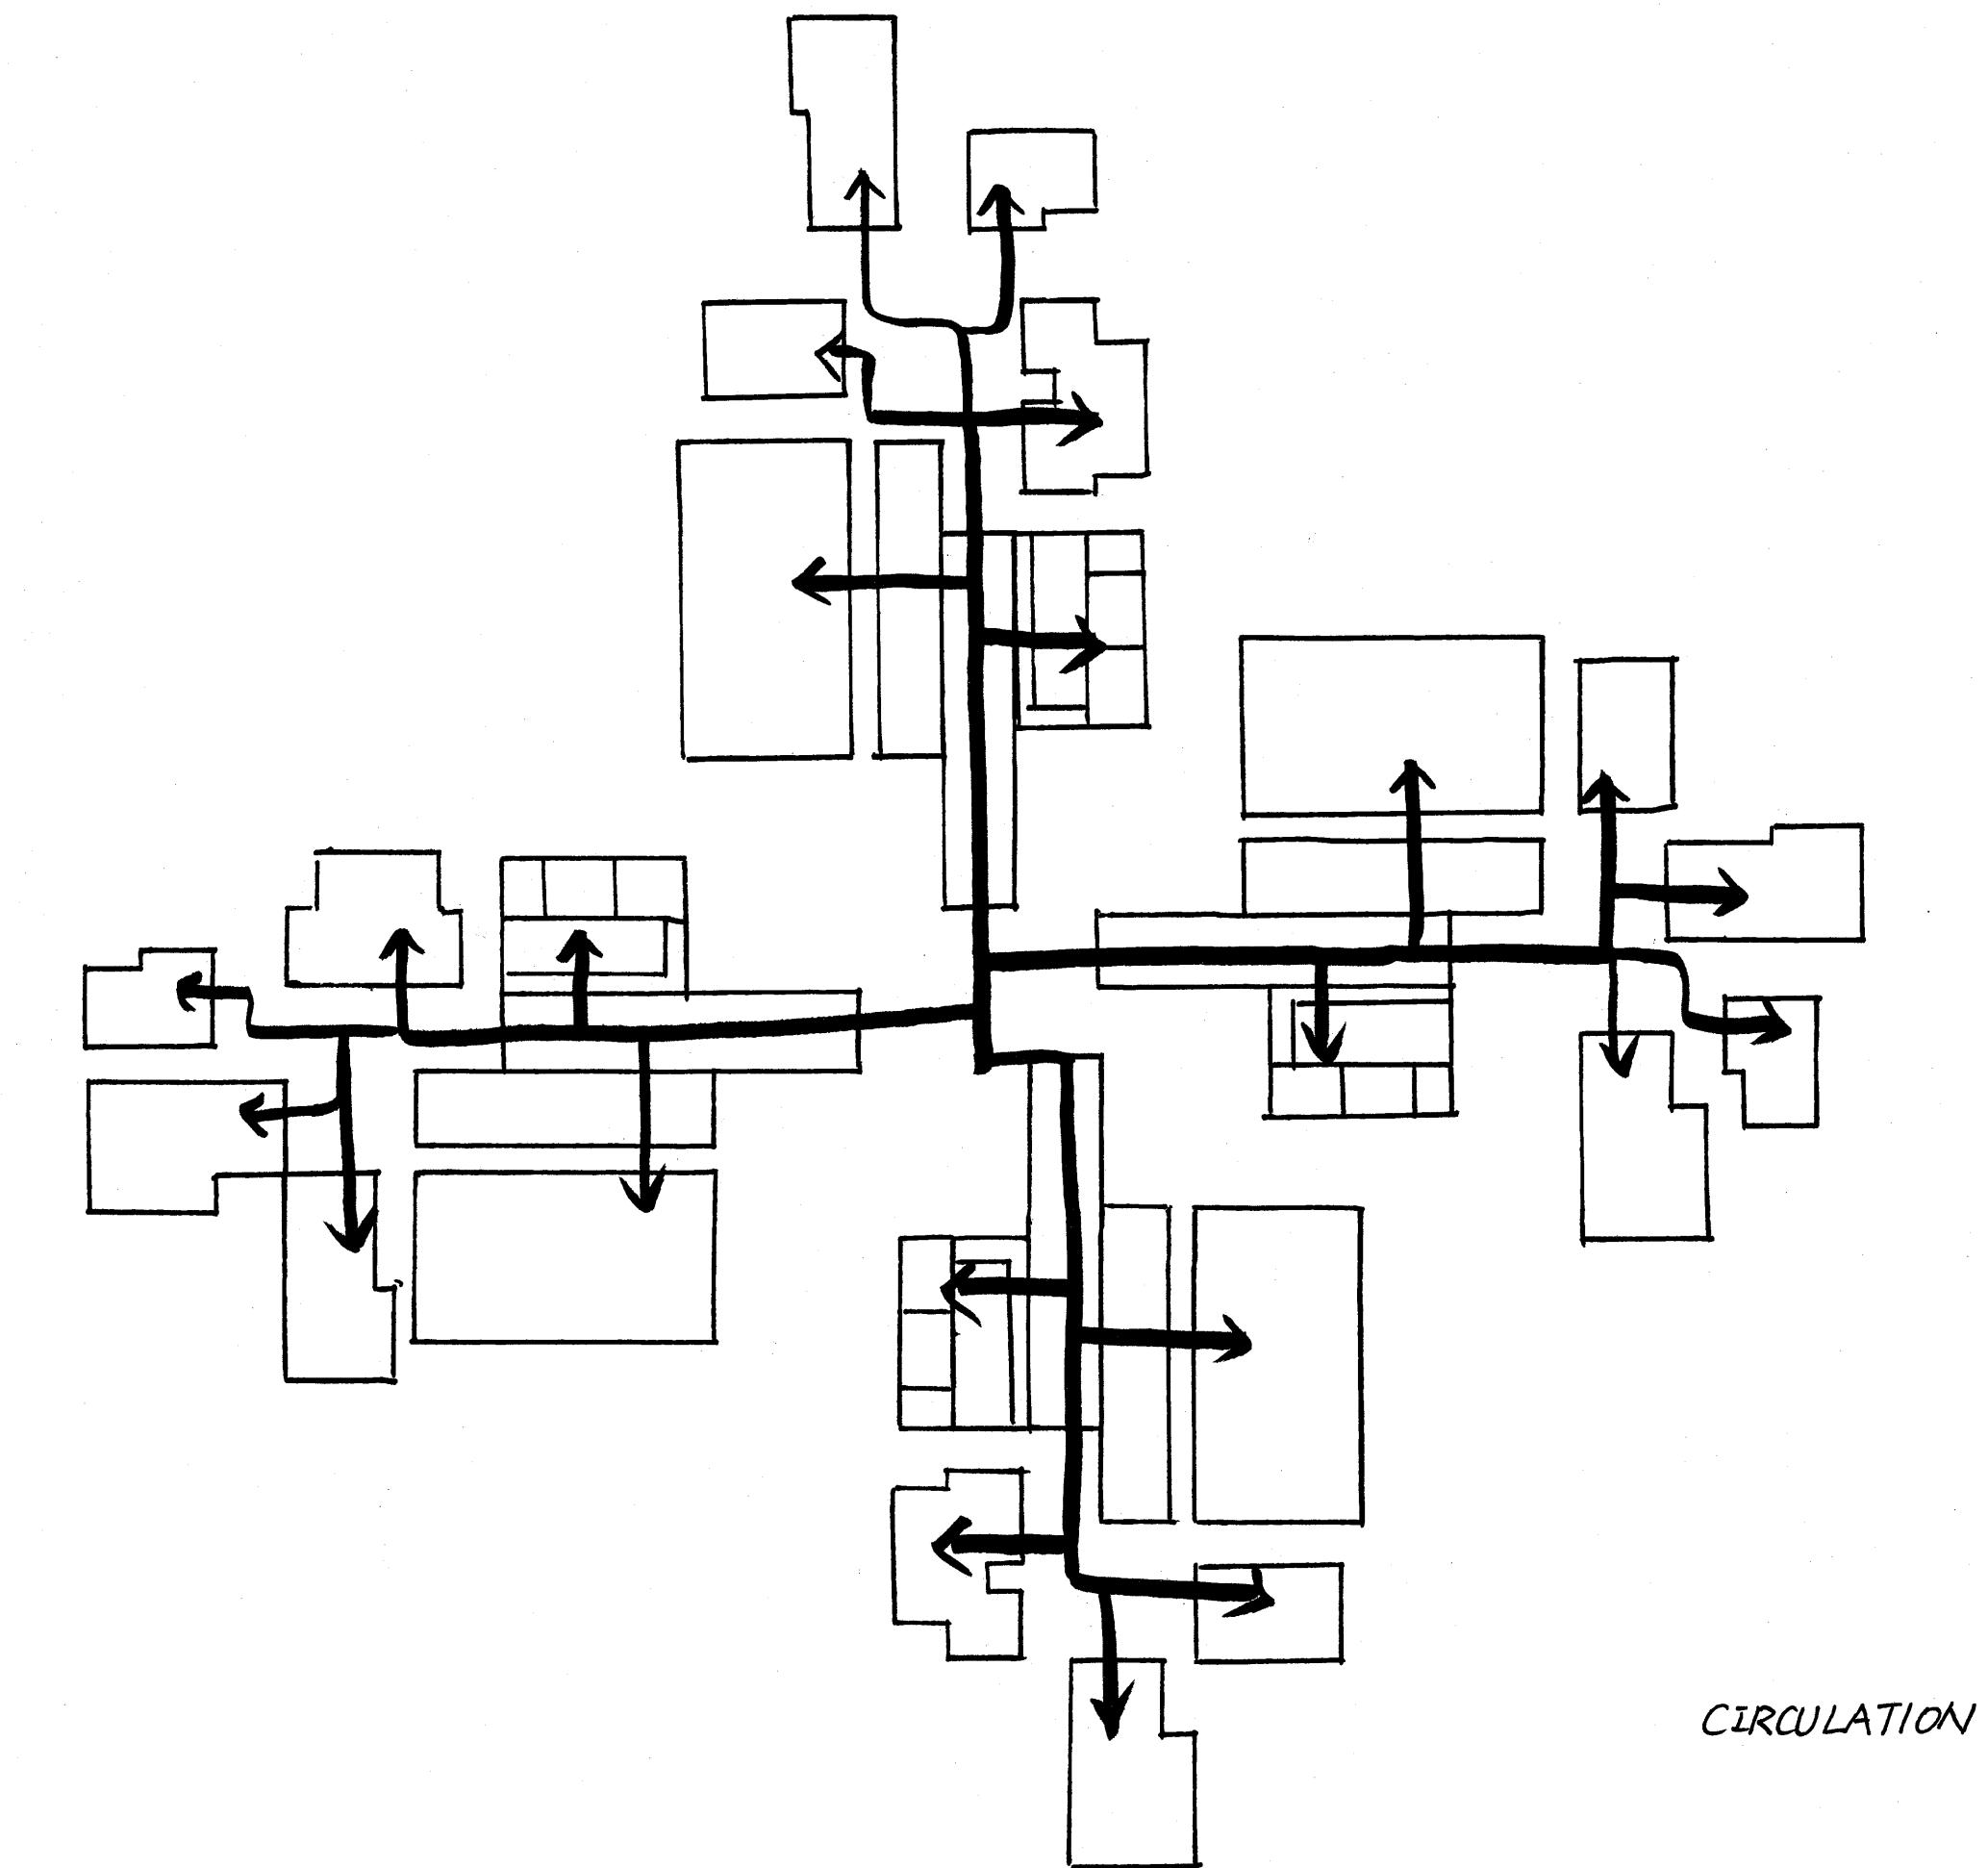


CIRCULATION

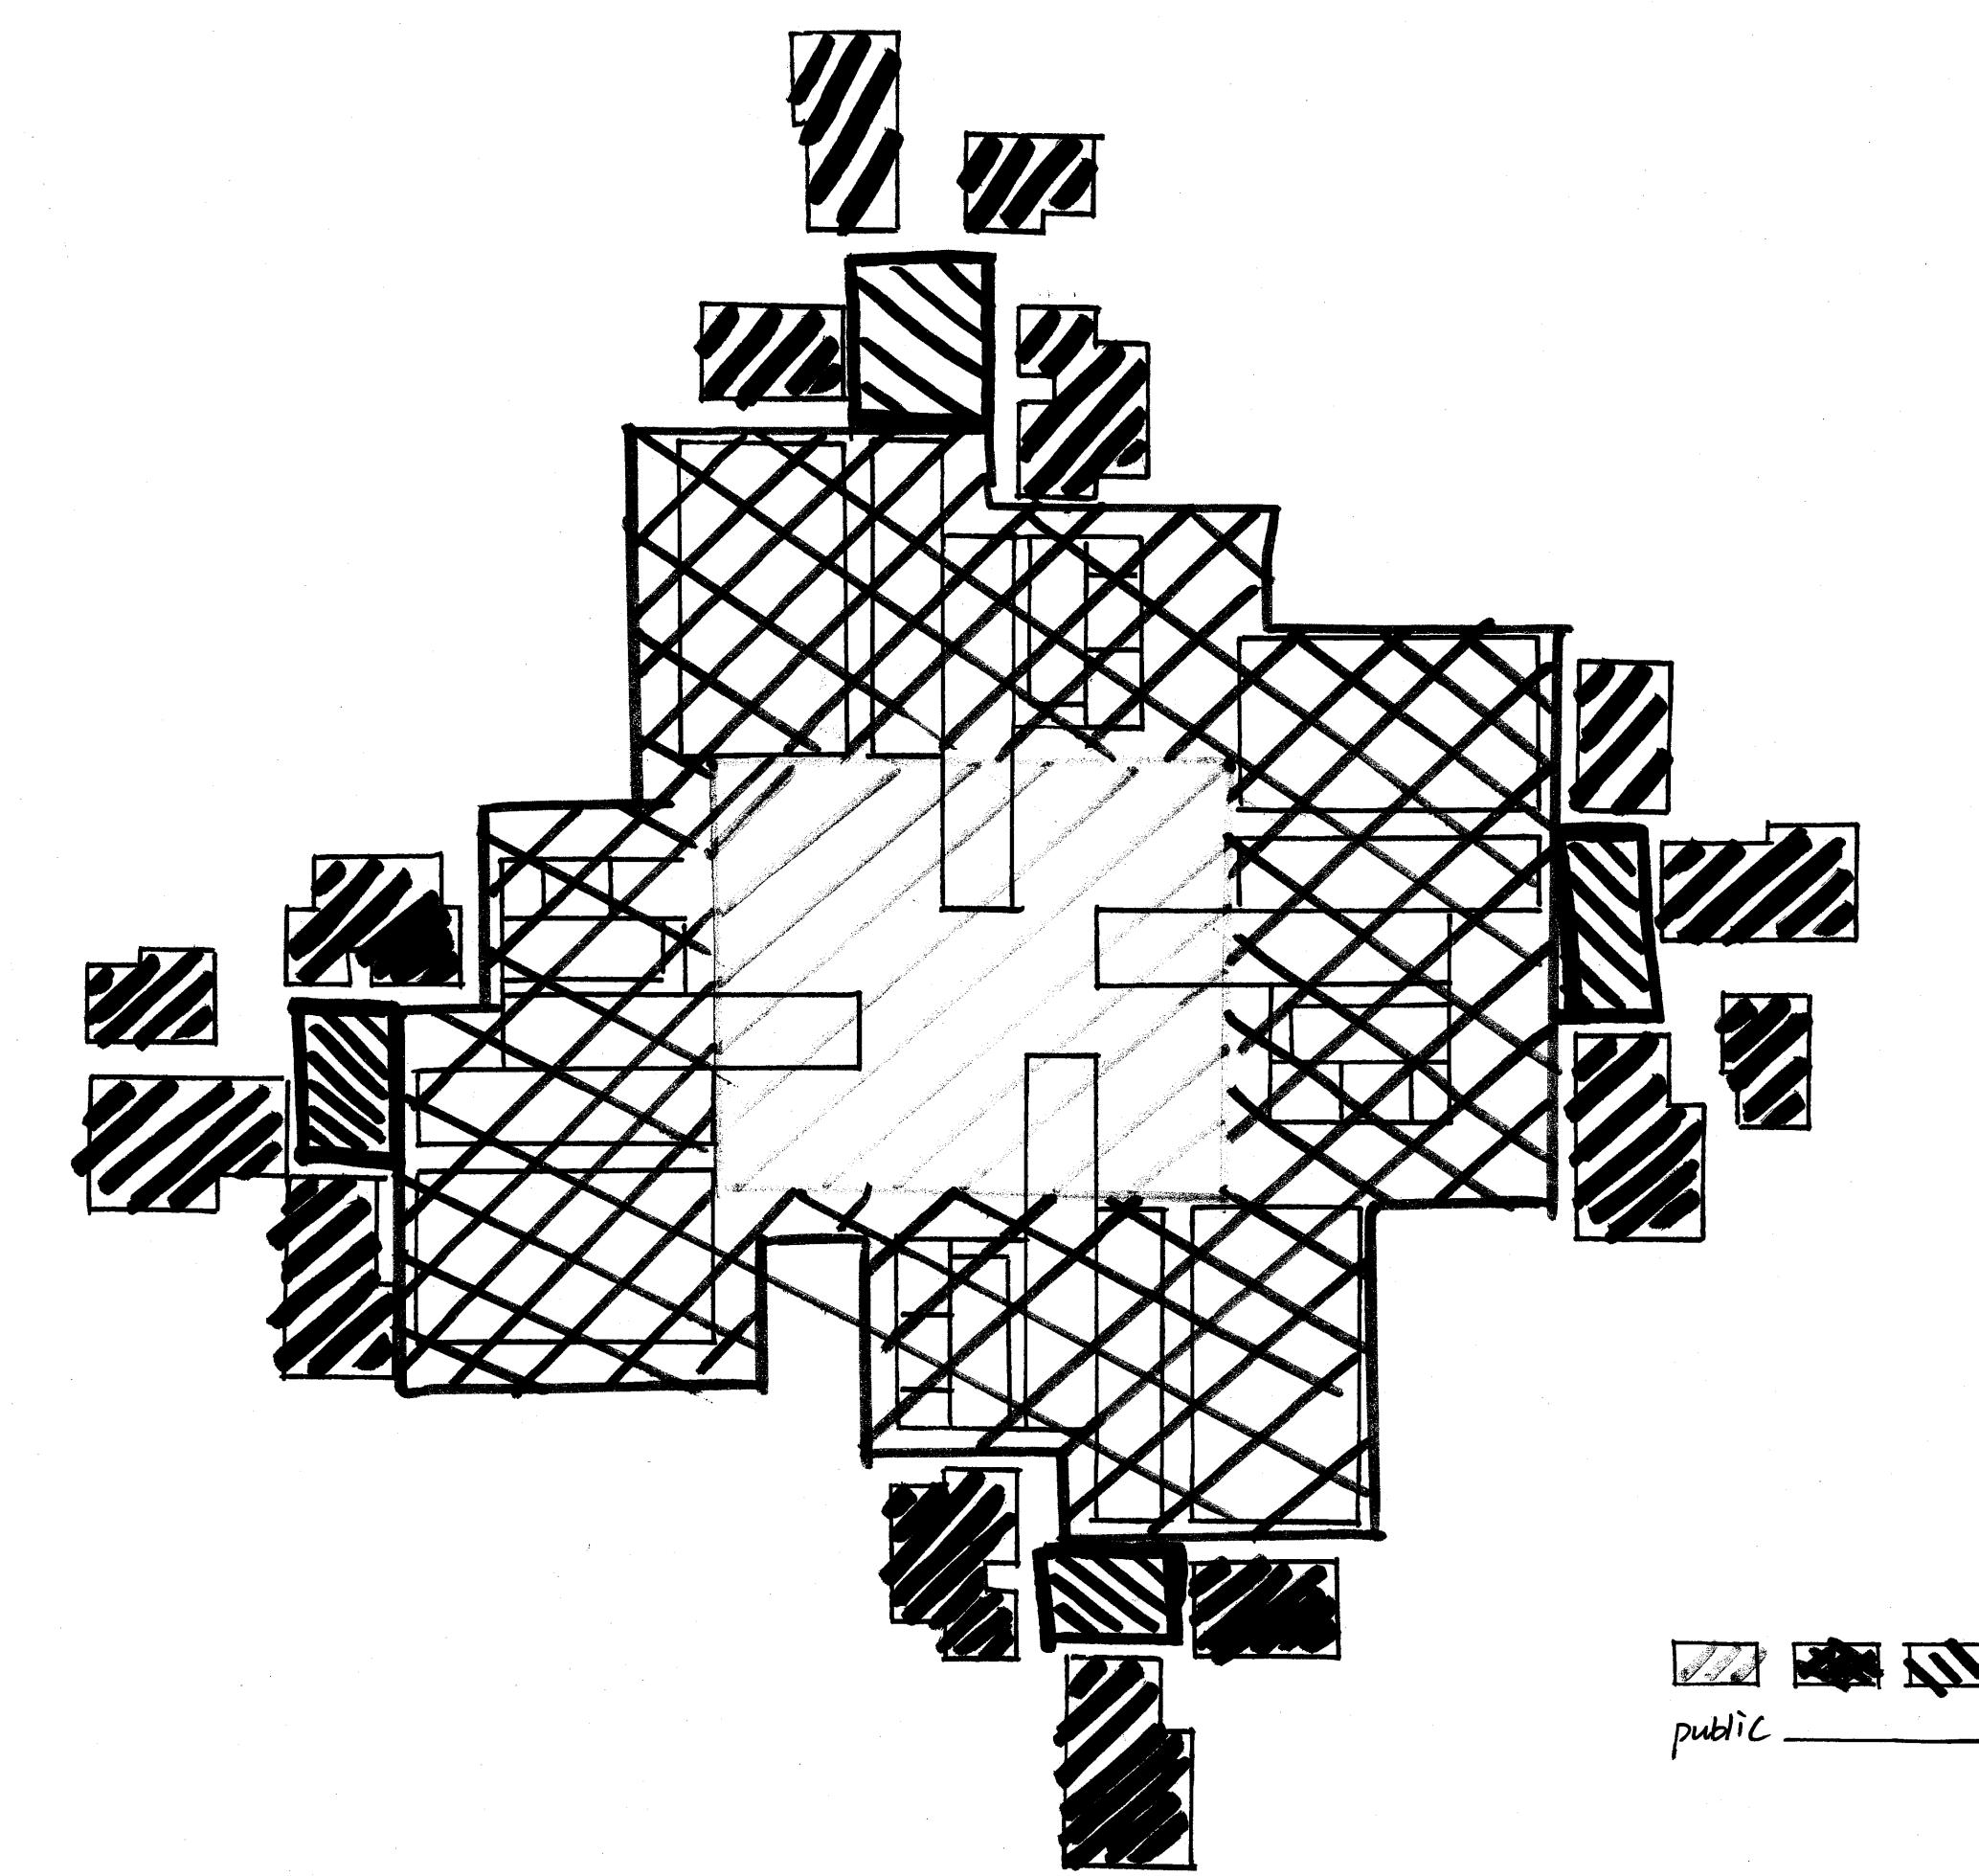

public → private

CONSTRUCTION

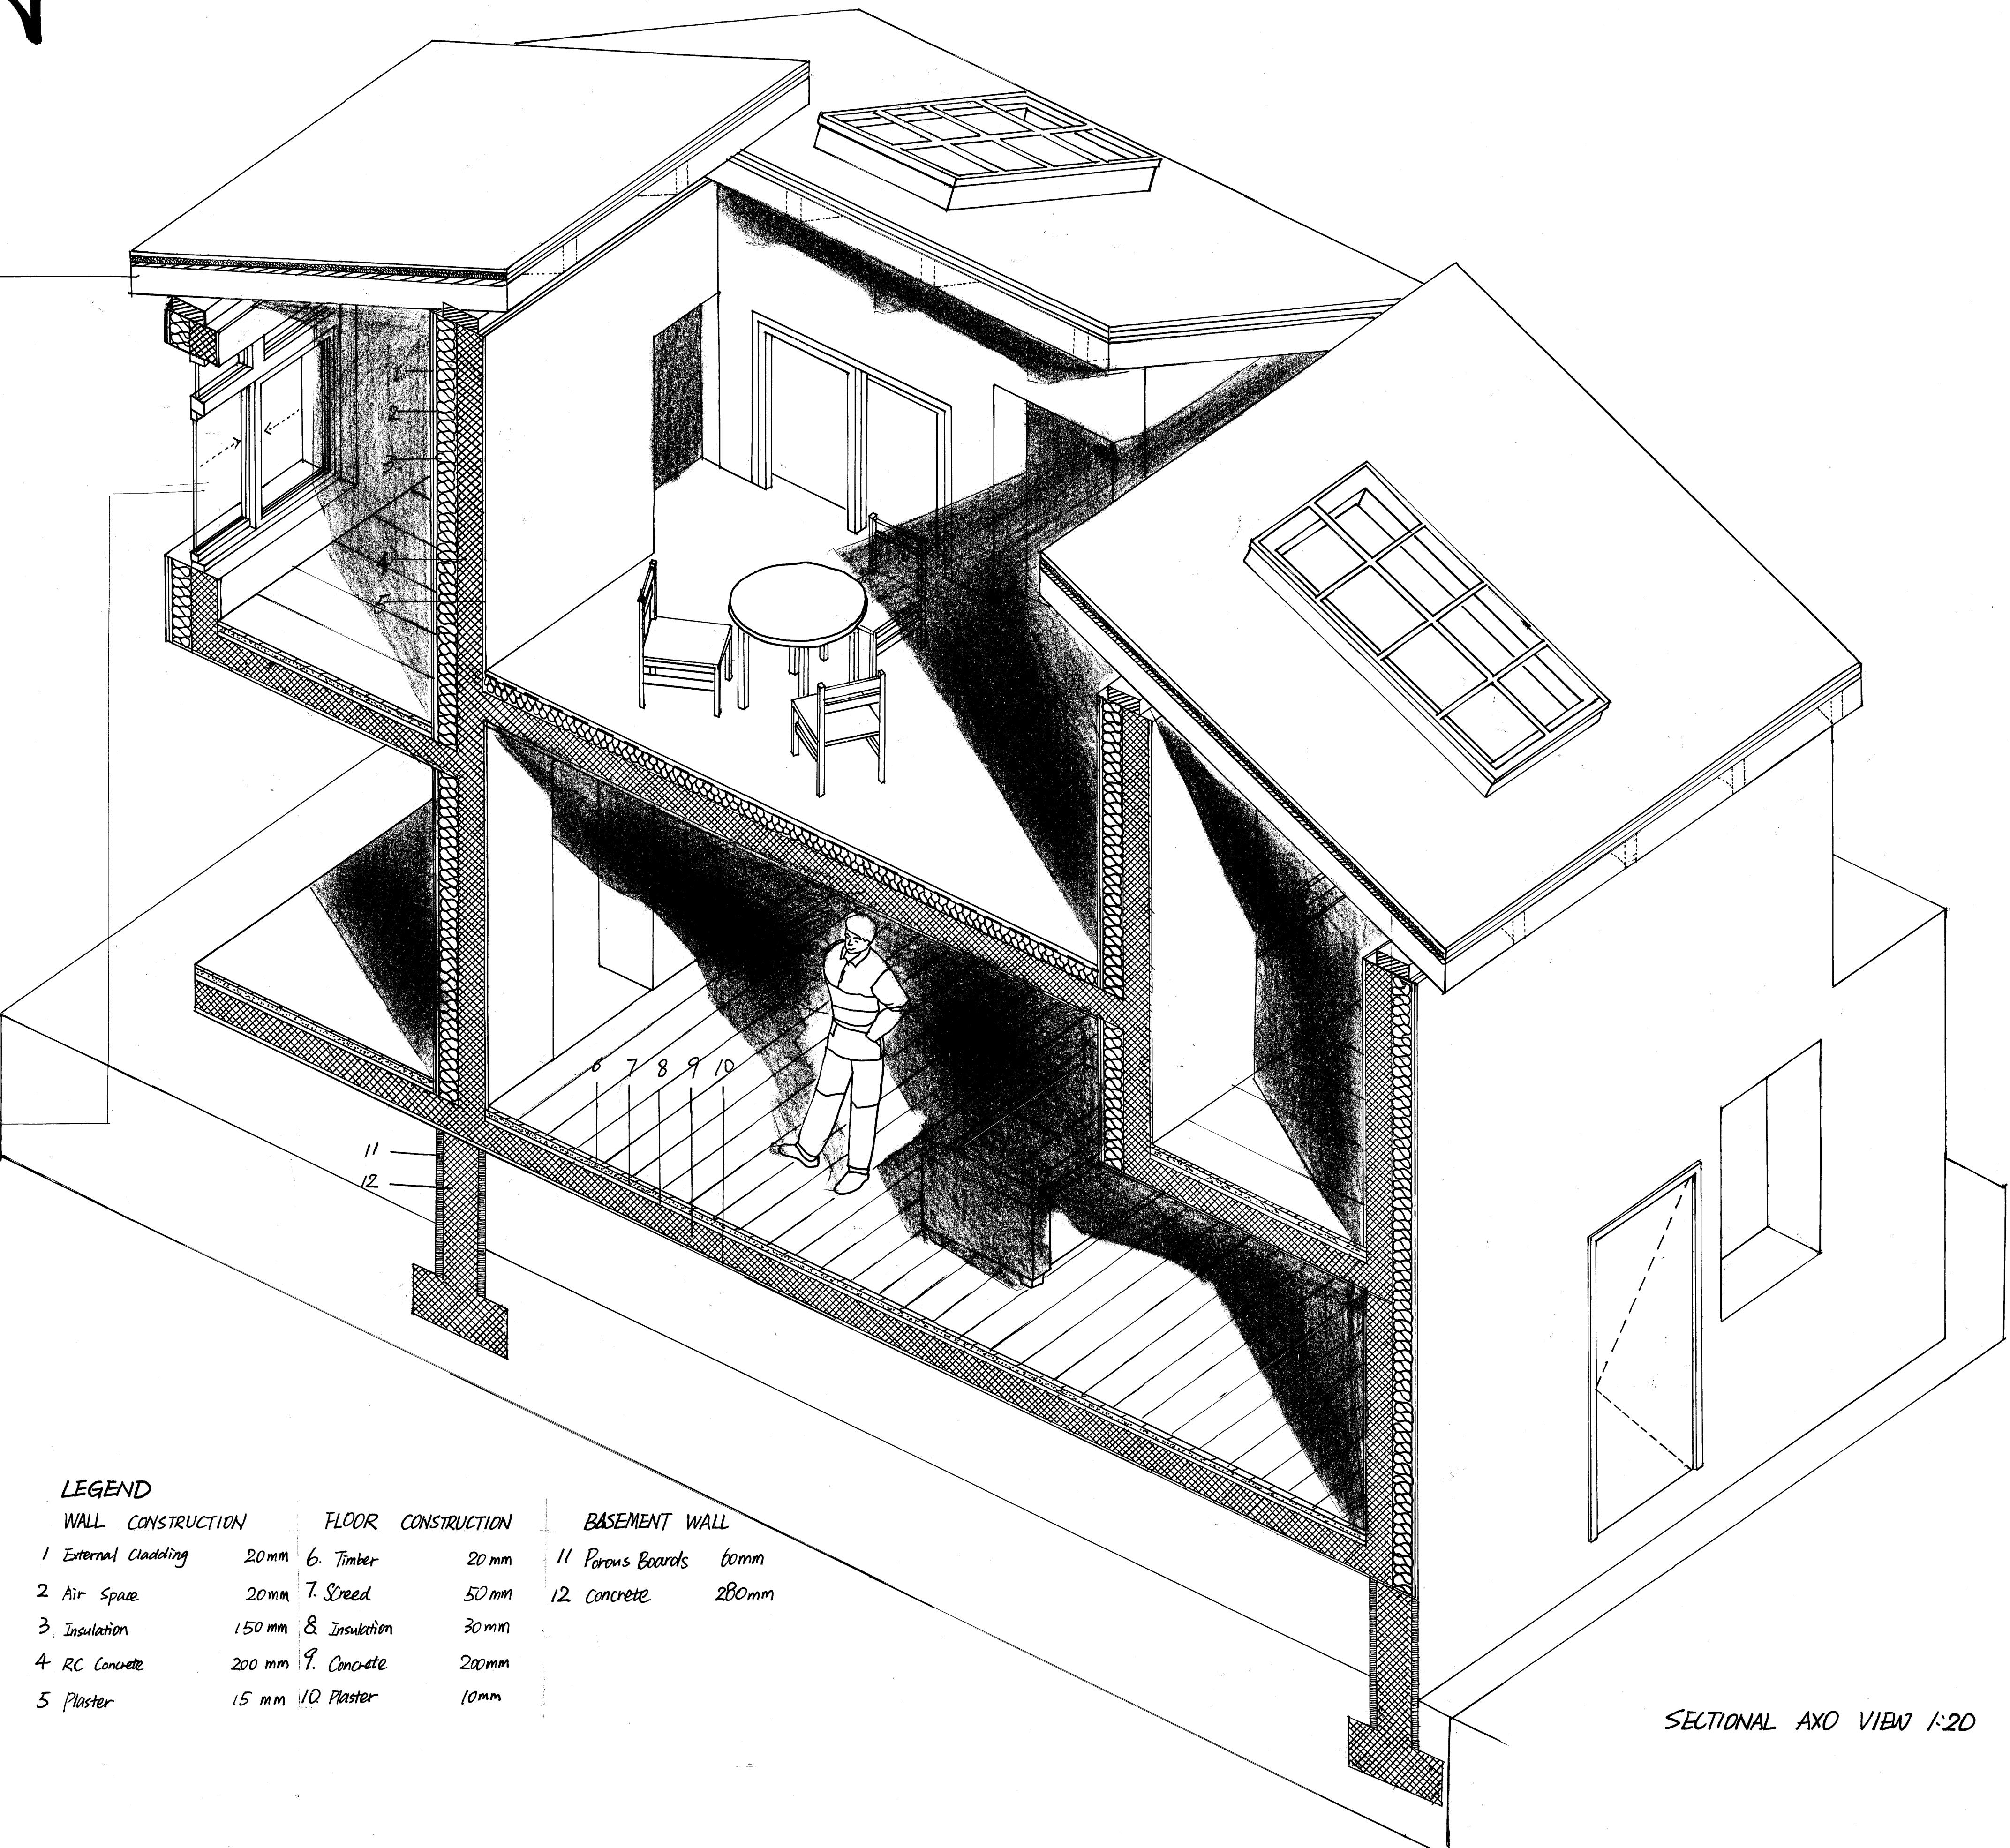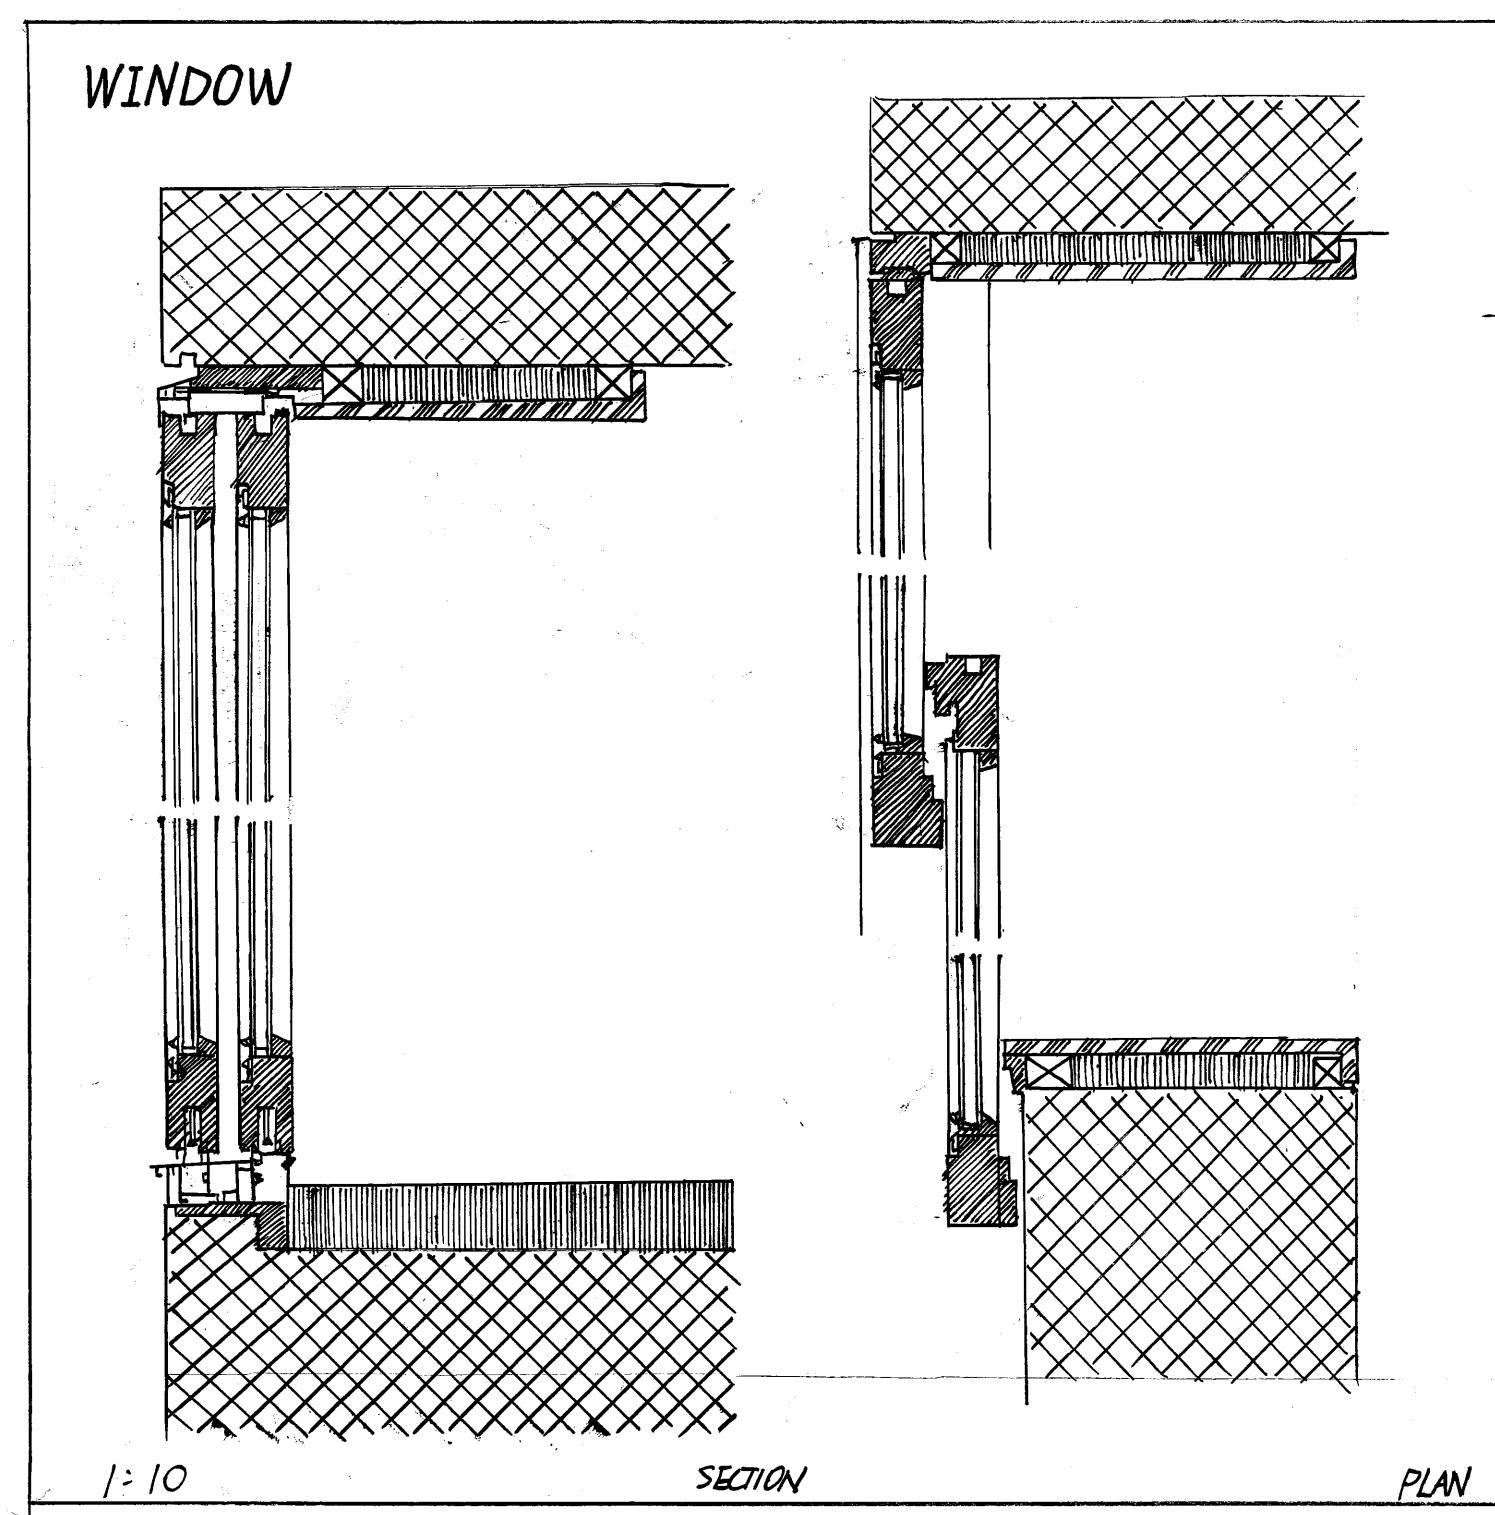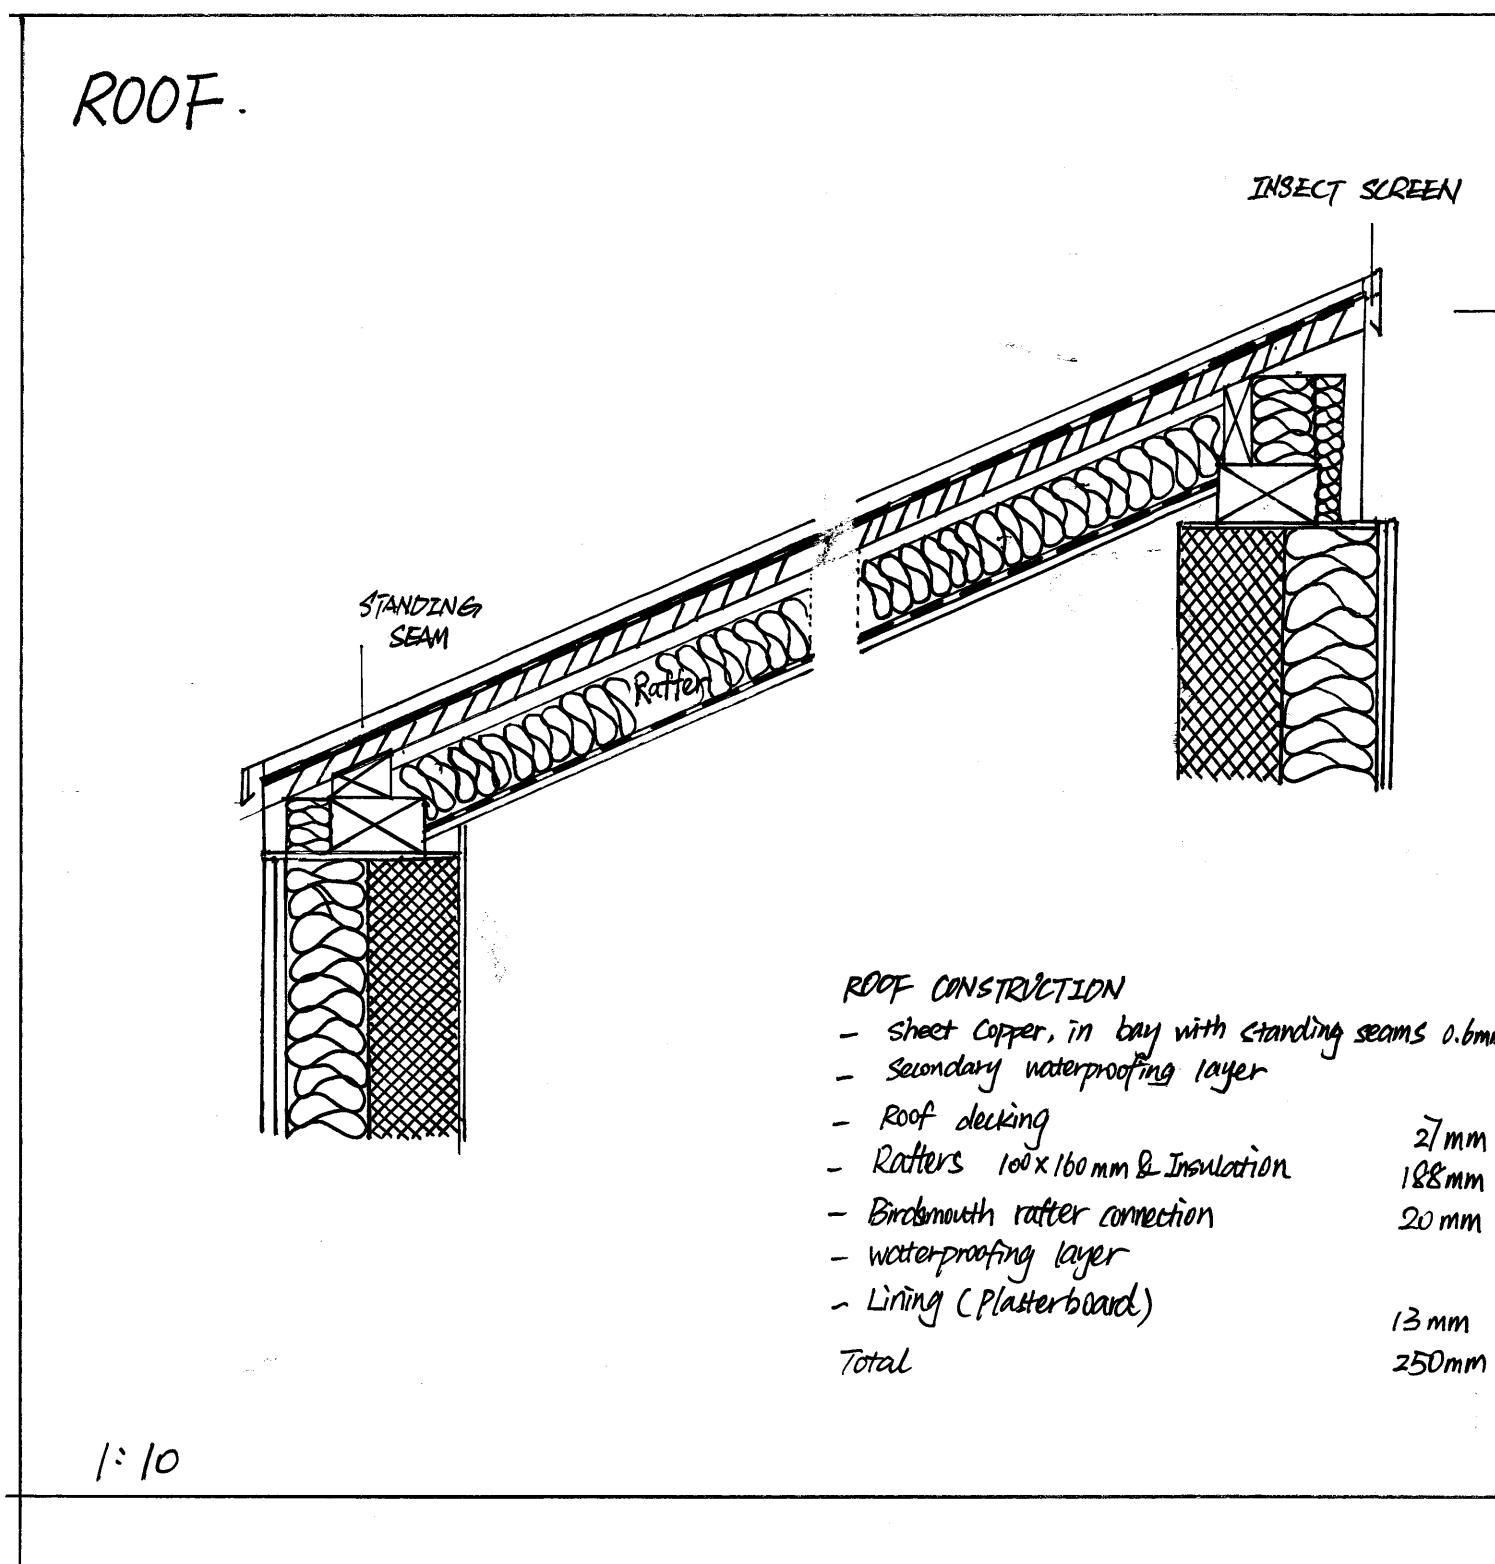

EXPERIENCE

